



COR 2Helix V1006/Logo-M-AE

Number of Pumps : 2

Rated Power : 2.2kW

Rated Current : 4.3A

Supply rating : 3 x400V 50Hz

Duty/Assist/Standby : 1D+1S

Starting Method : Multi VFD

IP rating : IP54

Ambient Temp. : 50 deg C

Article Number : XXXXX

Project Name : SAKHIR PROJECT

Application : Booster set


Additional Specification:

COR 2 HelixV1006 Logo-M -AE		A.N	 Wilo Middle East FZE Jebel Ali Free Zone–South PO Box 262720 Dubai UAE Tel: (+971 4) 880 91 77 Fax: (+971 4) 880 91 88. Ext. 122			
		CHECKED BY				
		S.S				
TITLE	PROJECT					
		DRAWN				
		6/15/2022				
CONSULTANT	CLIENT	DATE	SCALE	DRAWING NO	REV	PAGE
						1 /12


TECHNICAL DATA SHEET

ENCLOSURE SCHNEIDER ALFANAR LOCAL GRP MATERIALSHEET STEEL STAINLESS STEEL ALUMINUM GRP PRESENTATIONFIXED FRONT FUNCTIONAL DOOR PLAIN DOOR TRANSPARENT DOOR OTHER TYPE OF CONSTRUCTIONFORM - 1 FORM - 3 FORM - 4 DIMENSION (in mm)HEIGHT : 700 WIDTH : 600 DEPTH : 300COLOURRAL 7032 RAL 7035 MOUNTINGWALL FLOOR PEDESTAL INSTALLATIONINDOOR APPLICATION OUTDOOR APPLICATION						NEUTRAL/EARTH SYSTEM: DIRECT TO EARTH (TT) SEPARATE (TN-S) EARTHED (TN-C) ISOLATED (IT) BUS BARSHARD DRAWN HIGH CONDUCTIVITY COPPER ELECTROLYTICALLY TINNED BUSBARS SUITABLY SIZED MAIN(VER.) Size(XXXX) MAIN(HOR.) Size(XXXX) NEUTRAL Size(XXXX) EARTH Size(XXXX) BRANCH Size(XXXX) INSULATION VOLTAGE UPTO 600VCONNECTIONSTERMINATION DIRECT TO DEVICE THRU TERMINAL BLOCKS ACCESSFRONT REAR LEFT SIDE/ RIGHT SIDE CABLE ENTRYTOP BOTTOM SHROUDINGALL LIVE PARTS WIRINGCONTROL 1.0 Sqmm C.T WIRES 2.5Sqmm						AUXILIARY SUPPLY VOLTAGE 240V AC 220V AC 110V AC 24V AC 24V DC ORIGINEXTERNAL INTERNAL AUXILIARY TRANSFORMER AUXILIARY DC SOURCE CIRCUIT MARKINGWIRING >Power Cable :Phase : Upto - 16sqmm - Red, yellow, Blue Above 16sqmm - black cable with color code sleeveNeutral : BlackEarth : Yellow + GreenControl Cable :230V AC : Red+Black110V AC : Orange24VAC : Grey12V/24V DC : Blue(+), White(-)Volt Free contact : BrownLABELSFACIA LEGEND PLATES OF 1.5mm PRINTED PVC WITH WHITE LETTERS ON BLACK BACKGROUND ALL LABELS WITH CHAMFERED EDGES DANGER LABELS WITH WHITE LETTERS ON RED BACKGROUND						Standard Specification: Door interlock Isolator Motor overload protection Base load pump VFD control Pump run hour Equalizer Trip changeover standby changeover Dry run interlock System enable/disable Low/high pressure cutoff Door components: Run, Trip indication lamp HOA switch per pump BMS: VFC contact: Run, Trip, Auto per pump TYPE OF DRAWINGISSUED FOR APPROVALISSUED FOR PRODUCTIONAS BUILT DRAWING ALL DIMENSIONS ARE IN mm					
--	--	--	--	--	--	--	--	--	--	--	--	---	--	--	--	--	--	---	--	--	--	--	--


COR 2 HelixV1006 Logo-M -AE		A.N		 Wilo Middle East FZE Jebel Ali Free Zone–South PO Box 262720 Dubai UAE Tel: (+971 4) 880 91 77 Fax: (+971 4) 880 91 88. Ext. 122			
		CHECKED BY					
		S.S					
TITLE	PROJECT	DRAWN				000	2 /12
		6/15/2022					
CONSULTANT	CLIENT	DATE	SCALE	DRAWING NO		REV	PAGE

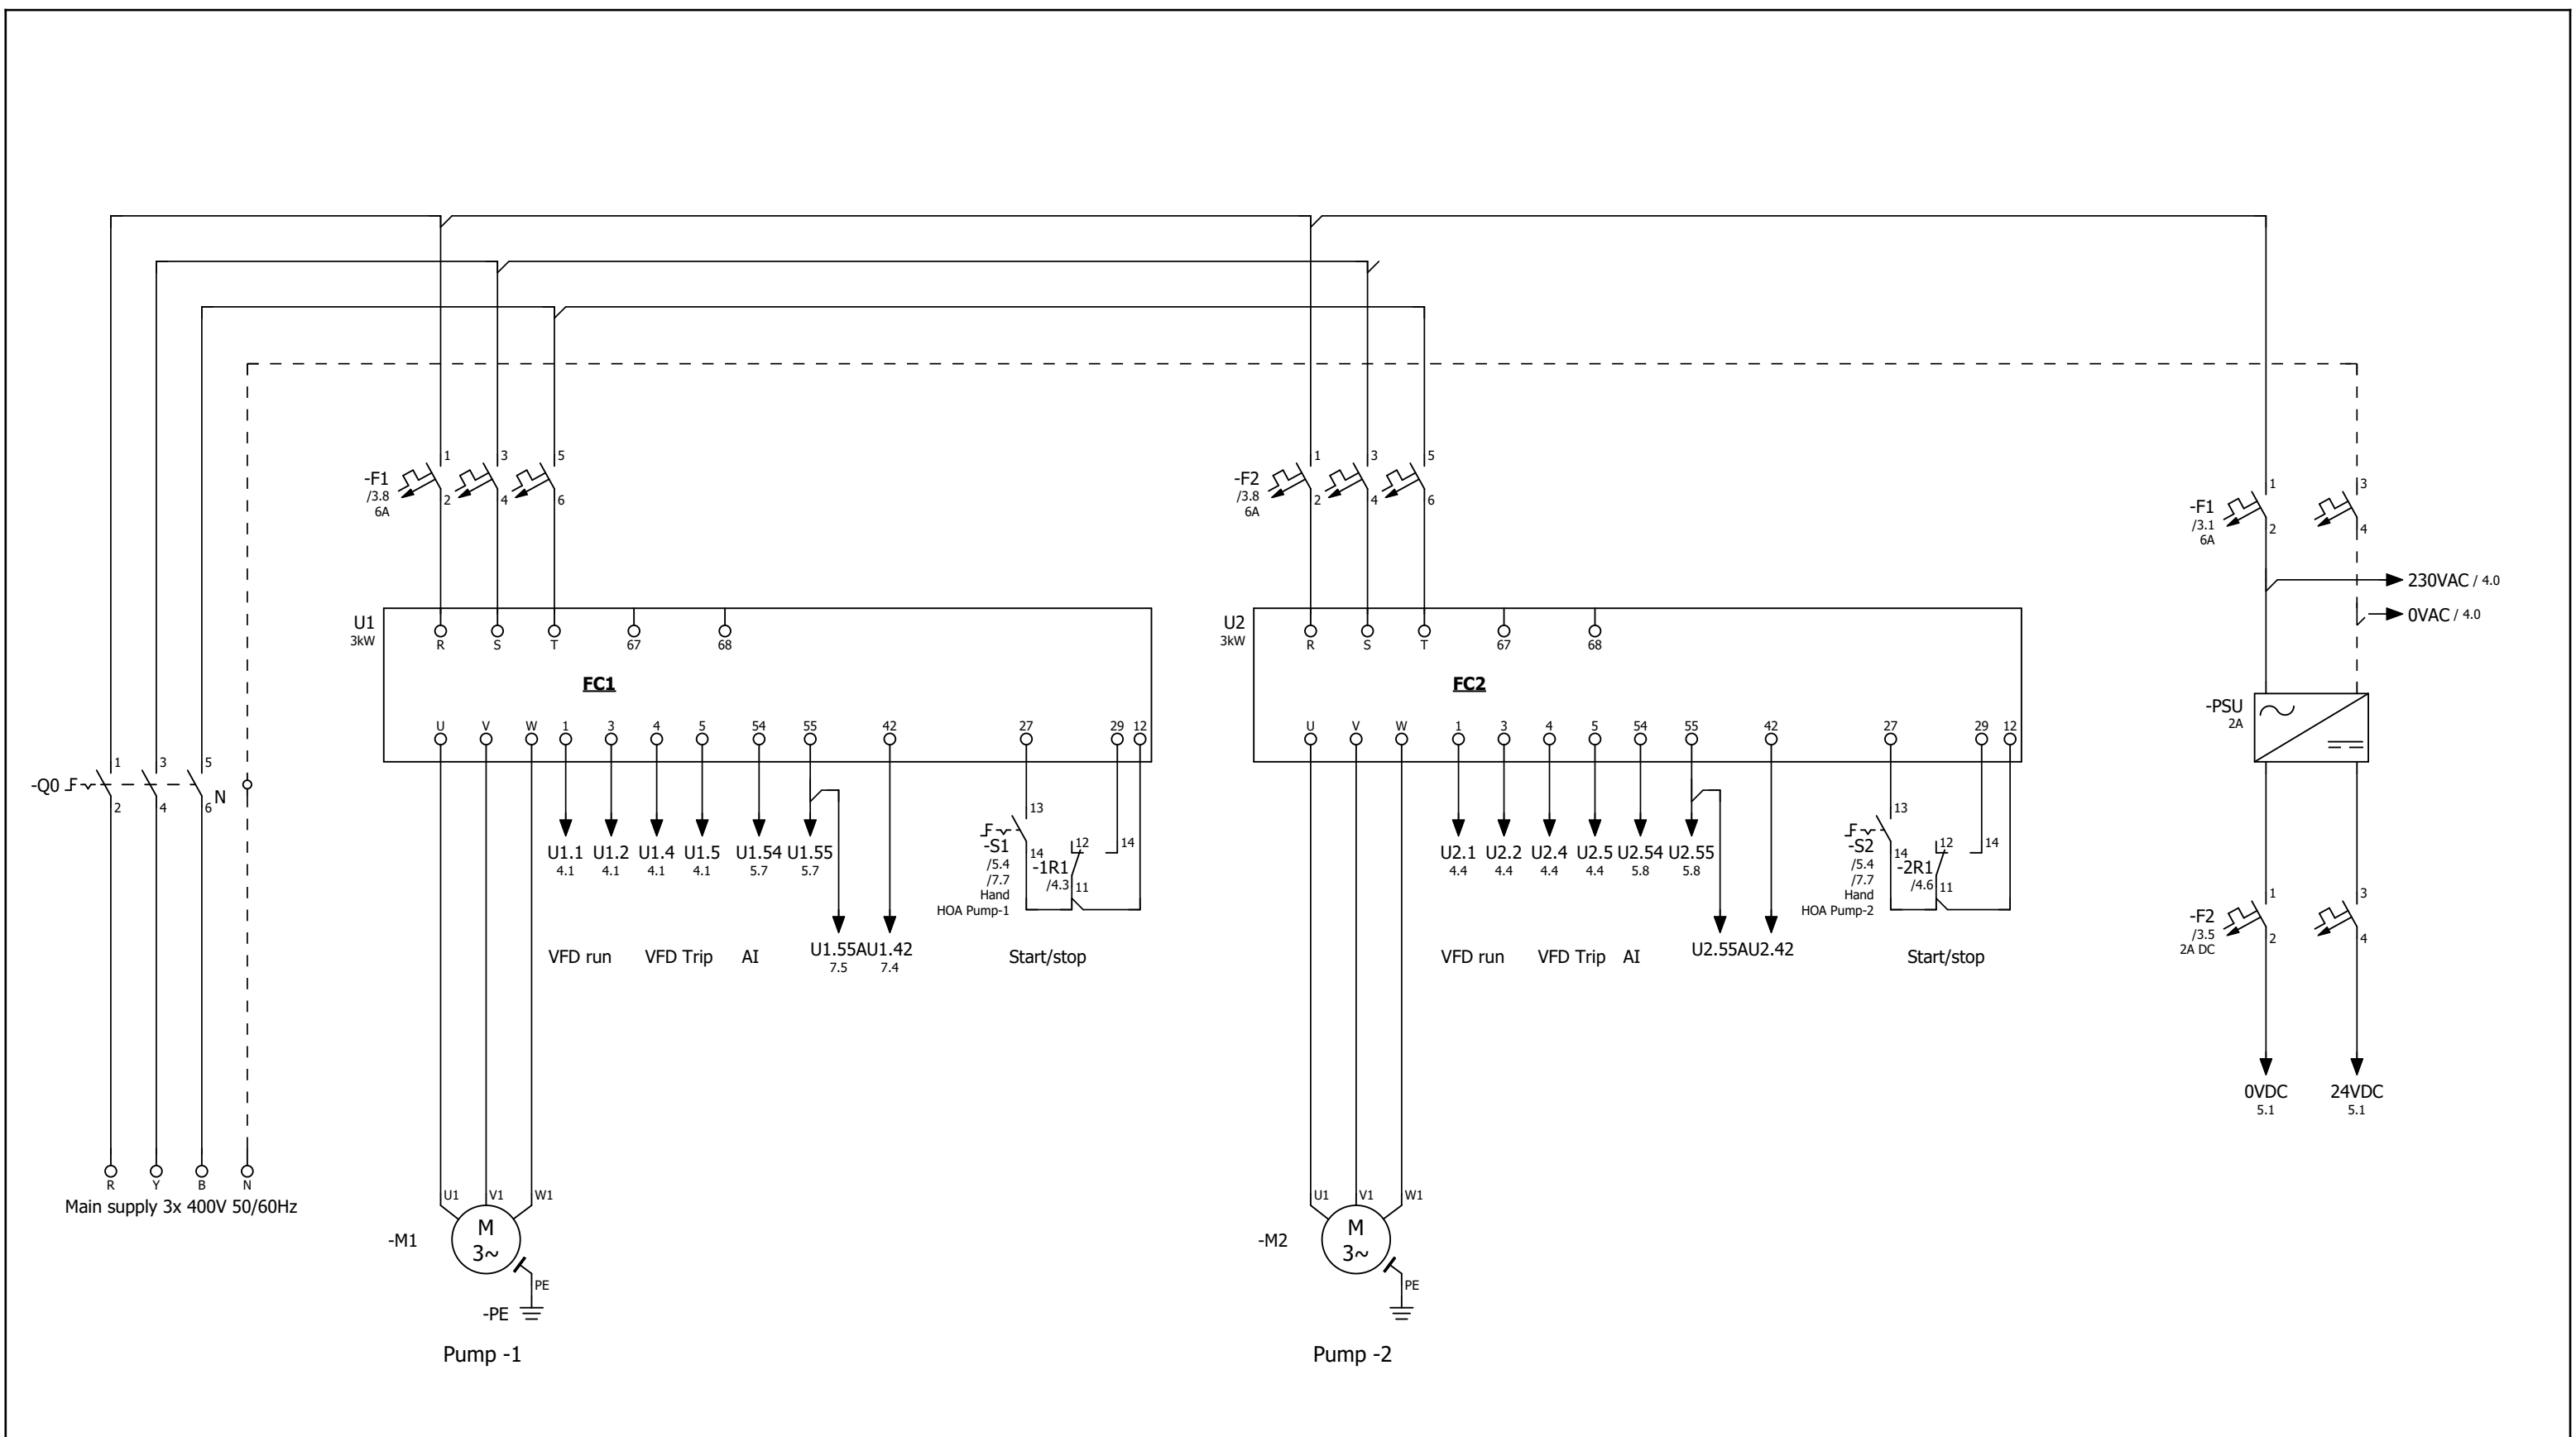

COR 2 HelixV1006 Logo-M -AE				A.N		wilo Wilo Middle East FZE Jebel Ali Free Zone–South PO Box 262720 Dubai UAE Tel: (+971 4) 880 91 77 Fax: (+971 4) 880 91 88. Ext. 122				
				CHECKED BY						
				S.S						
TITLE		PROJECT						DRAWN		
				6/15/2022						000
				CONSULTANT		CLIENT		DATE		SCALE

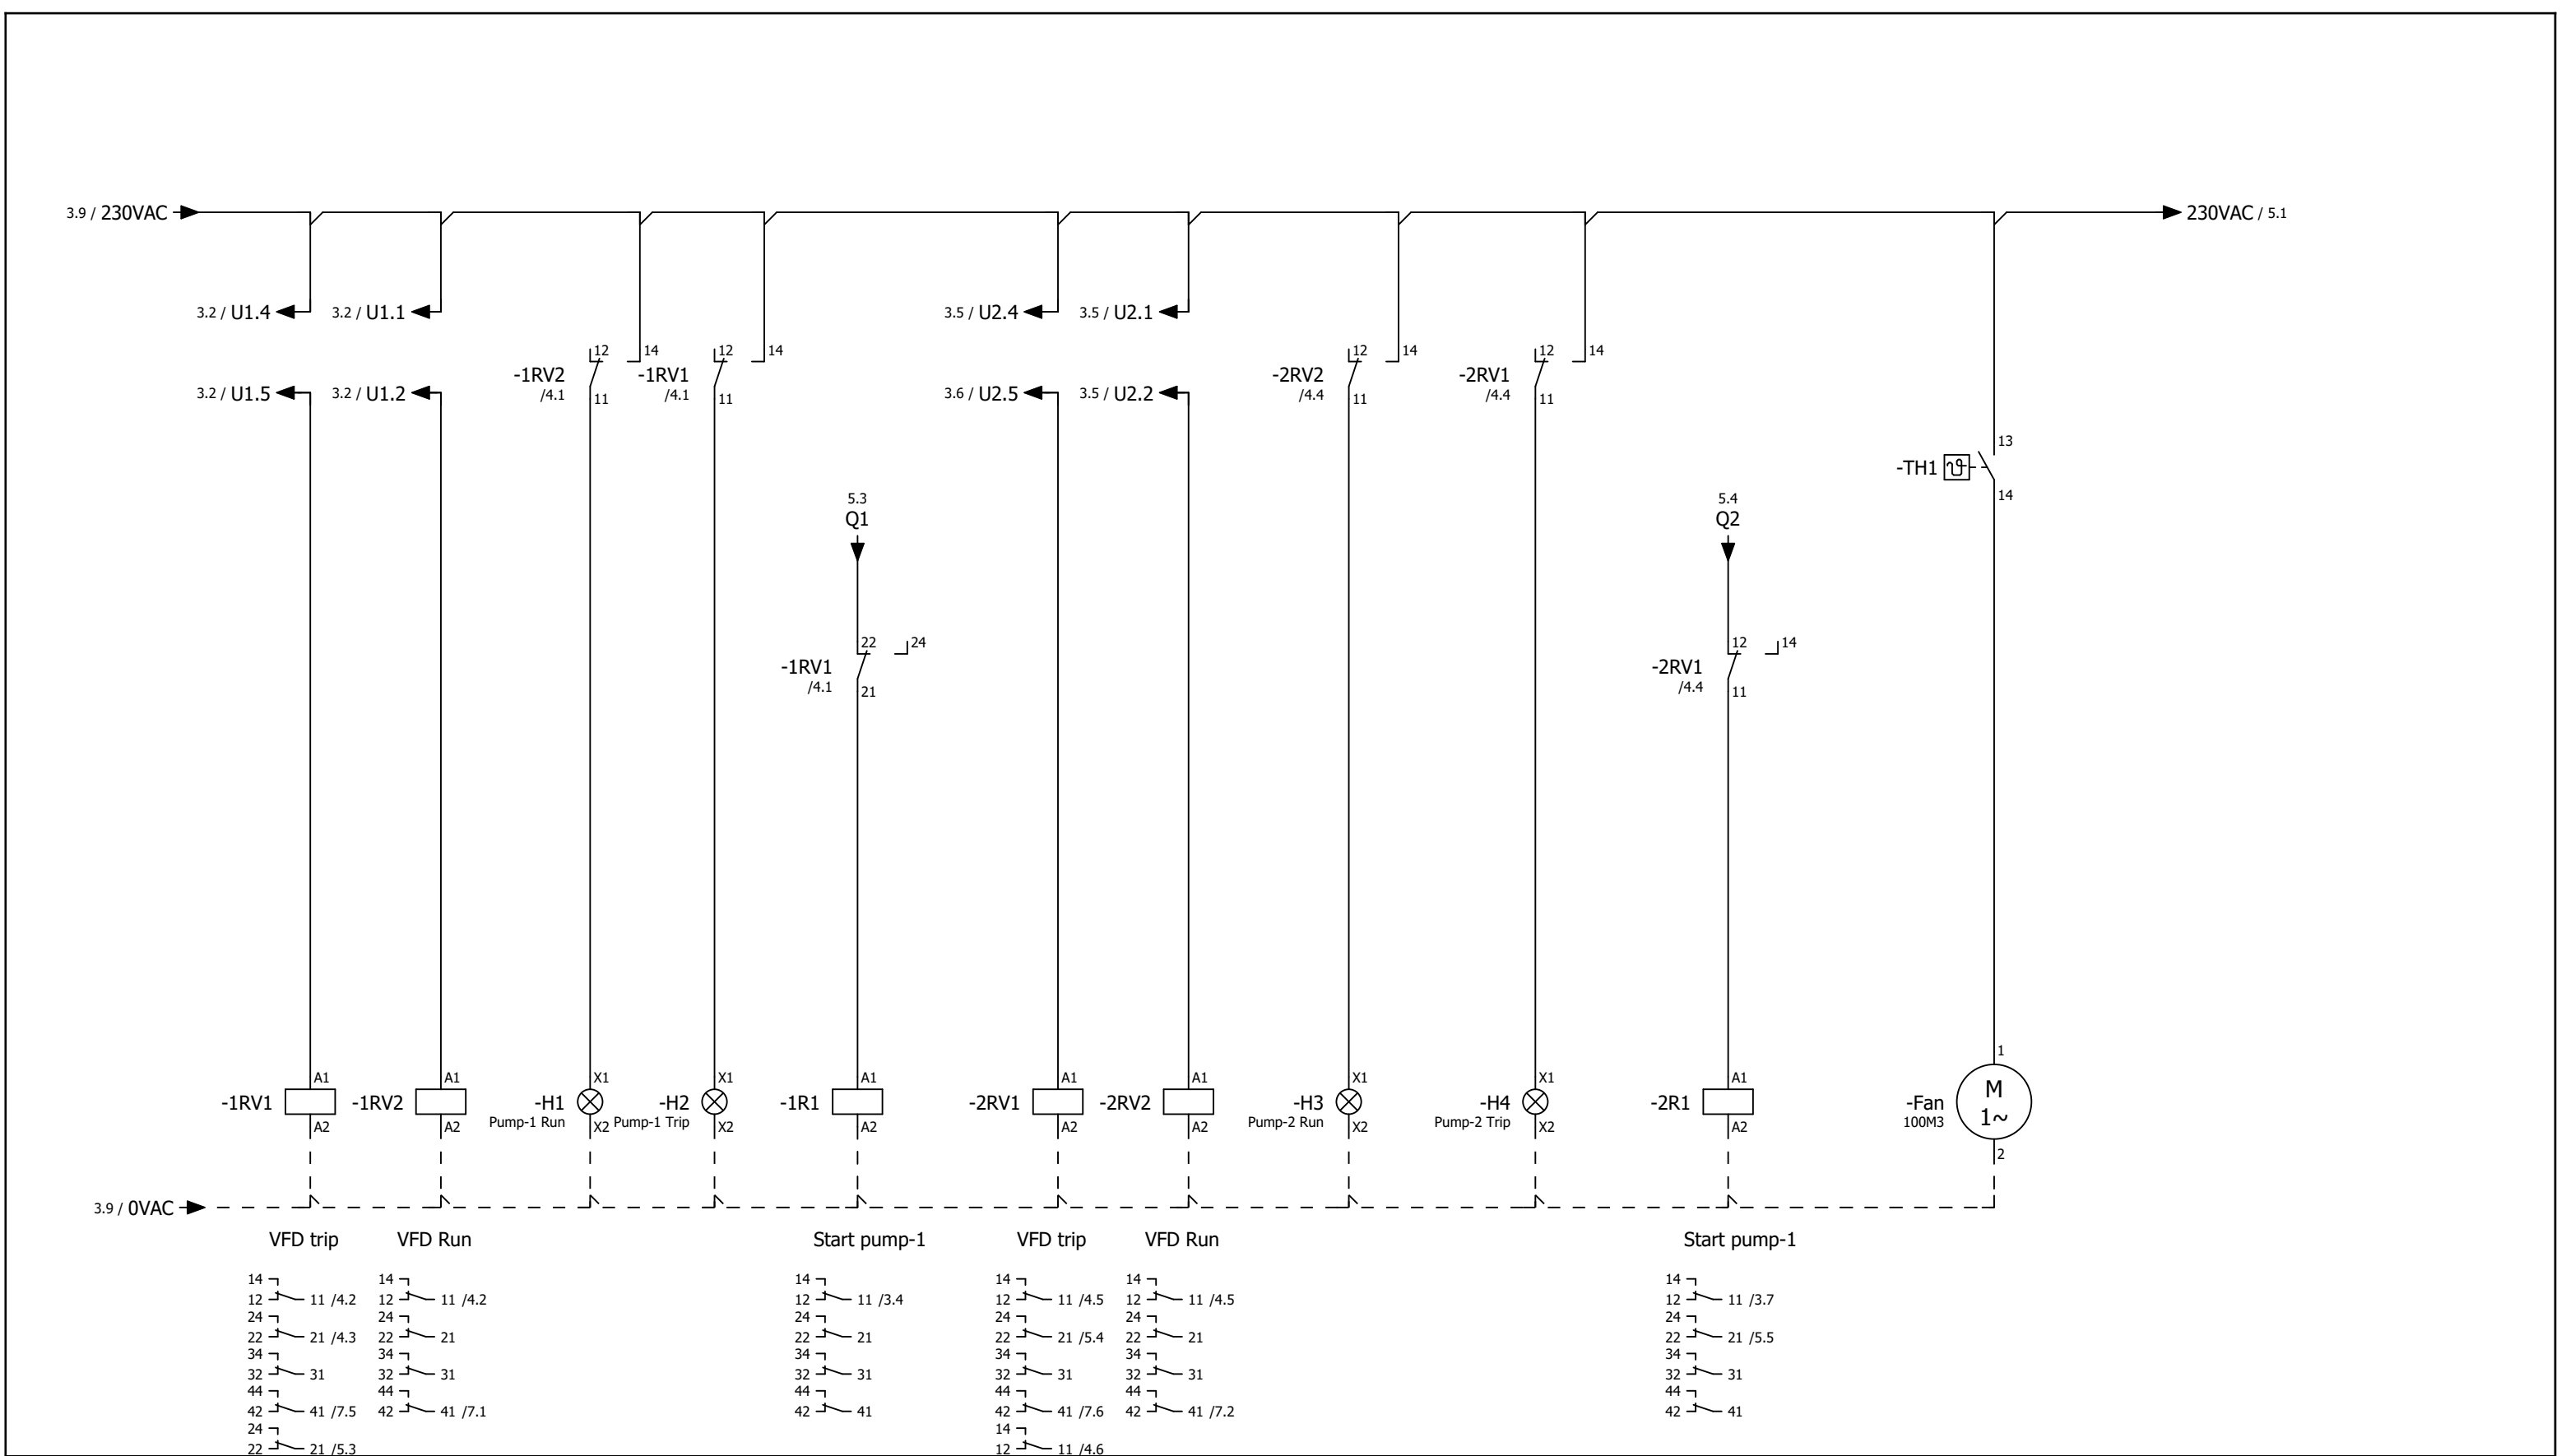


COR 2 HelixV1006 Logo-M -AE		A.N	wilo Wilo Middle East FZE Jebel Ali Free Zone-South PO Box 262720 Dubai UAE Tel: (+971 4) 880 91 77 Fax: (+971 4) 880 91 88. Ext. 122			
		CHECKED BY				
		S.S				
TITLE	PROJECT		DRAWN			
CONSULTANT	CLIENT	DATE	SCALE	DRAWING NO	REV	PAGE

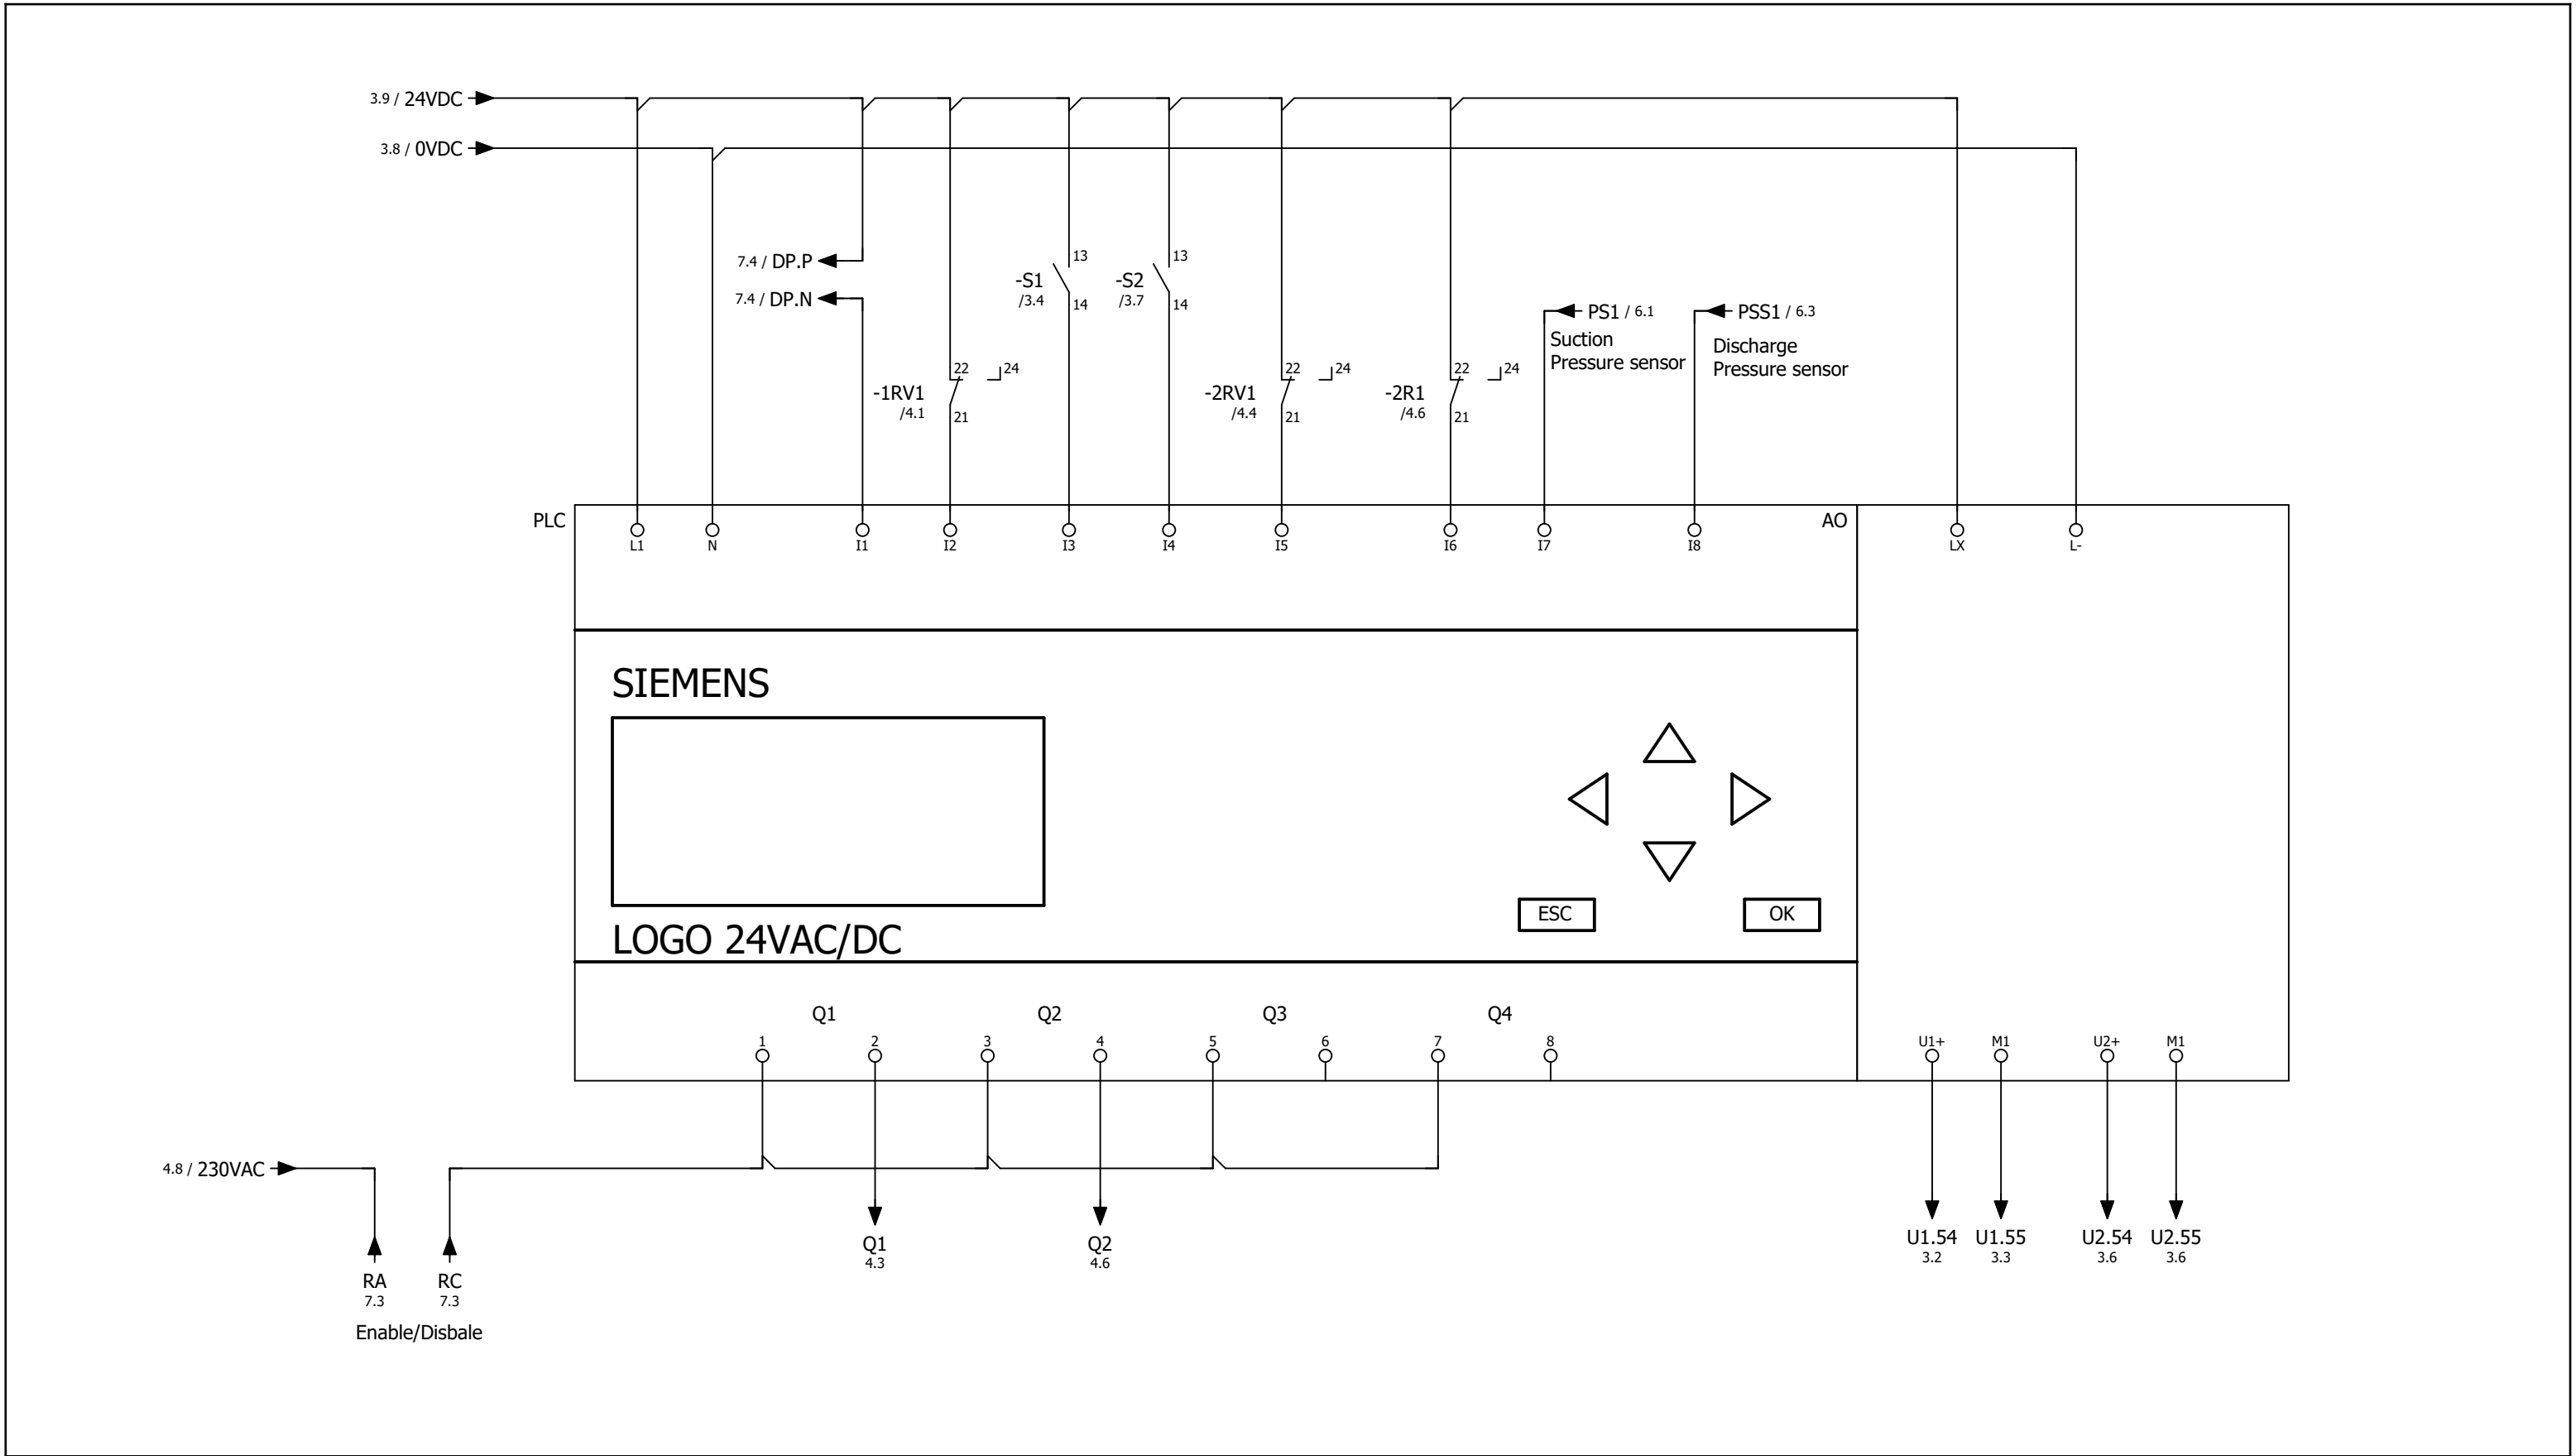


COR 2 HelixV1006 Logo-M -AE		A.N	 Wilo Middle East FZE Jebel Ali Free Zone–South PO Box 262720 Dubai UAE Tel: (+971 4) 880 91 77 Fax: (+971 4) 880 91 88. Ext. 122			
		CHECKED BY				
		S.S				
TITLE	PROJECT					
		DRAWN			000	5 /12
		6/15/2022				
CONSULTANT	CLIENT	DATE	SCALE	DRAWING NO	REV	PAGE


Pressure Transmitter Signal:

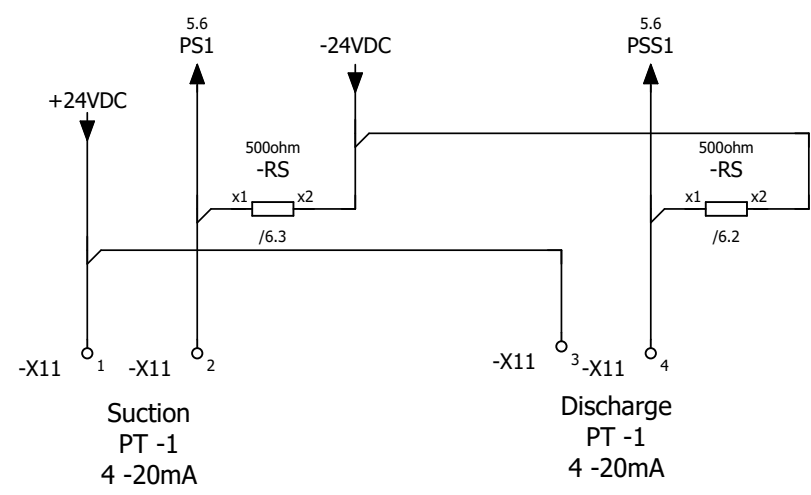


COR 2 HelixV1006 Logo-M -AE		A.N	wilo Wilo Middle East FZE Jebel Ali Free Zone-South PO Box 262720 Dubai UAE Tel: (+971 4) 880 91 77 Fax: (+971 4) 880 91 88. Ext. 122			
		CHECKED BY				
		S.S				
TITLE	PROJECT	DRAWN			000	6 /12
		6/15/2022				
CONSULTANT	CLIENT	DATE	SCALE	DRAWING NO	REV	PAGE

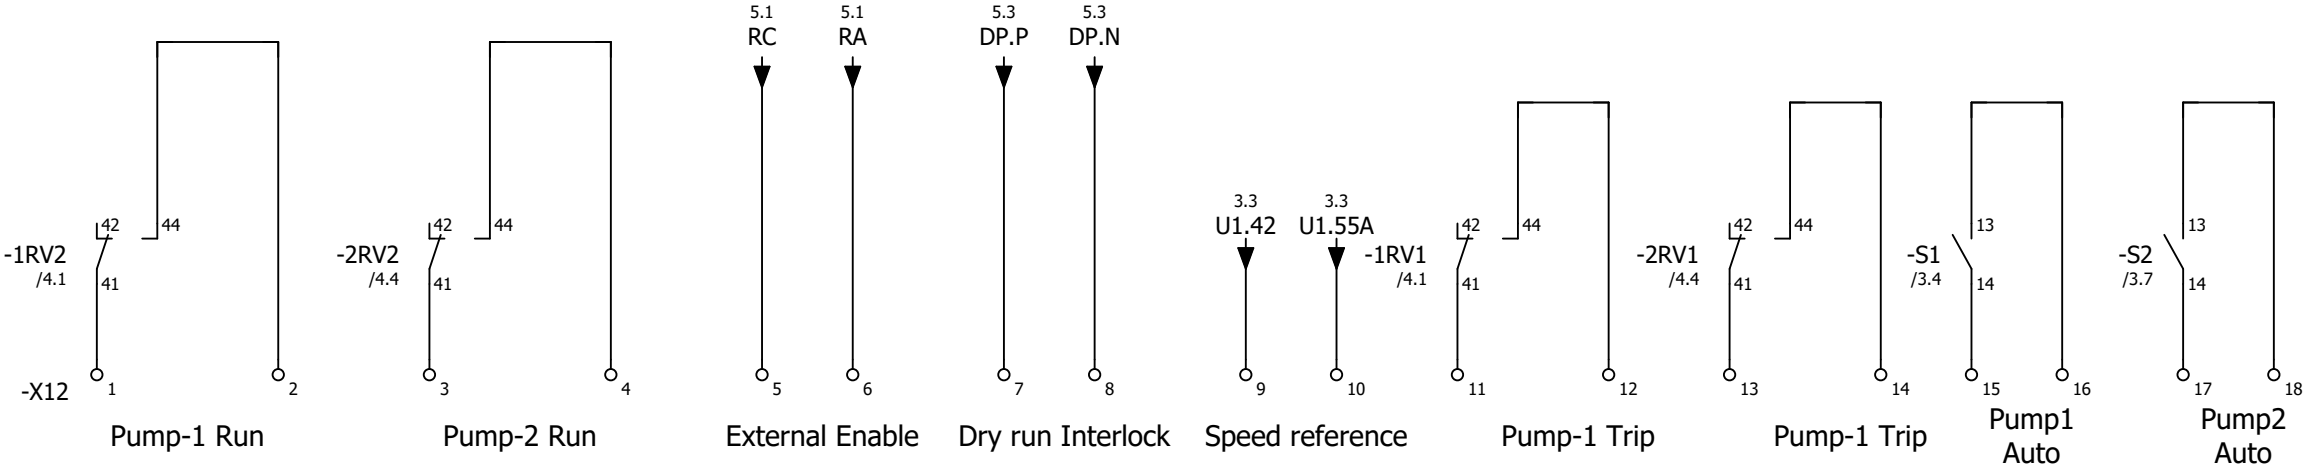


COR 2 HelixV1006 Logo-M -AE		A.N	wilo Wilo Middle East FZE Jebel Ali Free Zone–South PO Box 262720 Dubai UAE Tel: (+971 4) 880 91 77 Fax: (+971 4) 880 91 88. Ext. 122			
		CHECKED BY				
		S.S				
TITLE	PROJECT	DRAWN				000
		6/15/2022				
CONSULTANT	CLIENT	DATE	SCALE	DRAWING NO	REV	PAGE

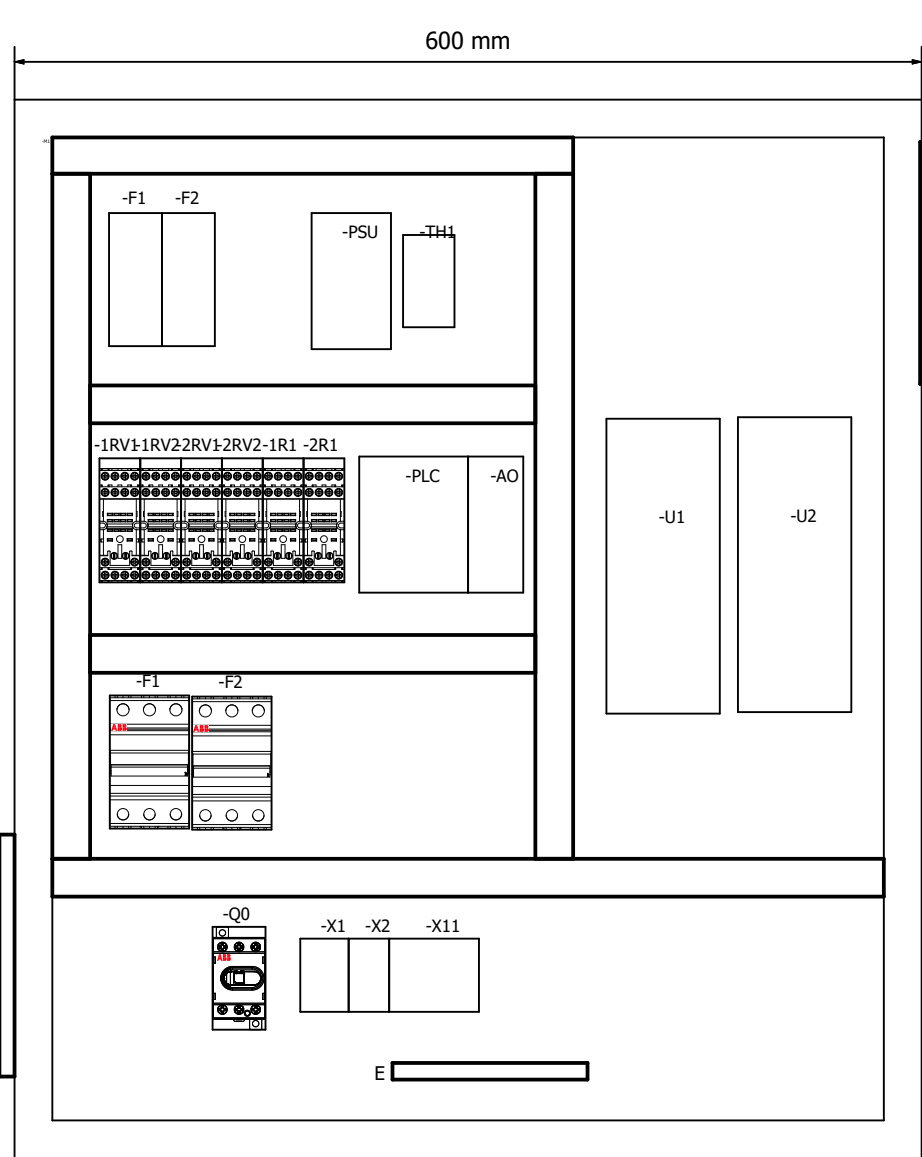

Internal View

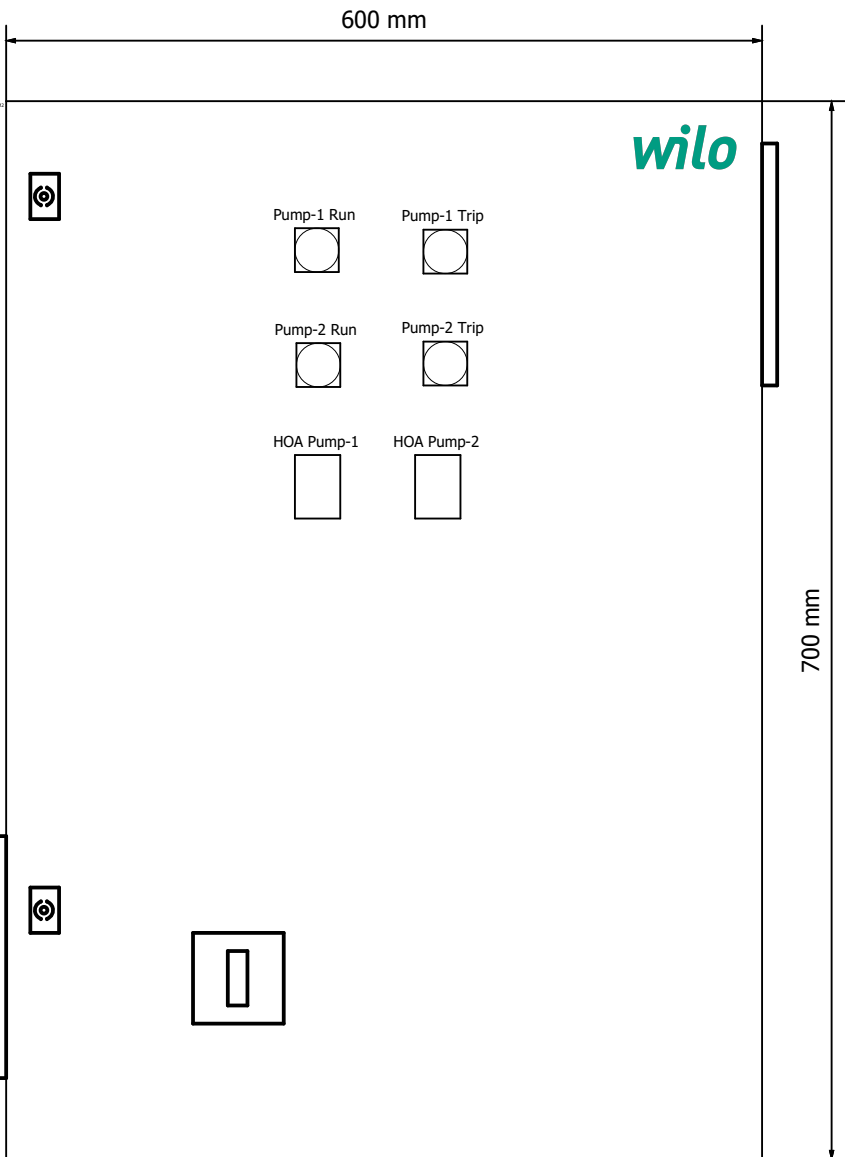

Front Fascia

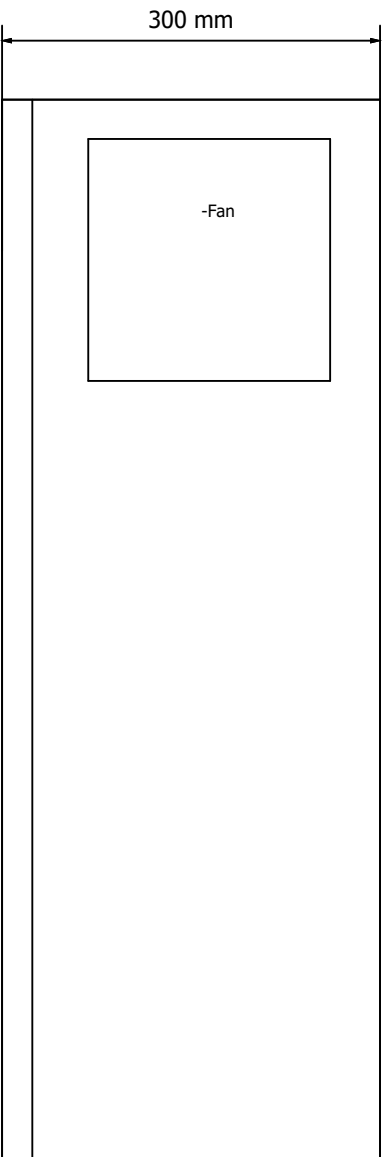

Side view

COR 2 HelixV1006 Logo-M -AE		A.N	wilo Wilo Middle East FZE Jebel Ali Free Zone–South PO Box 262720 Dubai UAE Tel: (+971 4) 880 91 77 Fax: (+971 4) 880 91 88. Ext. 122				
		CHECKED BY					
		S.S					
TITLE	PROJECT		DRAWN			000	8 /12
	6/15/2022						
CONSULTANT	CLIENT	DATE	SCALE	DRAWING NO	REV	PAGE	

Summarized parts list

Device Tag	Quantity	Designation	Type number	Order number	Supplier
AO	1	LOGO! AM2 AQ expansion module, PS: 24 V DC, 2 AO, 0-10 V, 0/4-20 mA for LOGO! 8	6ED1055-1MM00-0BA2	6ED1055-1MM00-0BA2	SIE
-F1;-F2	2	Miniature Circuit Breaker - S200P - 3P - C - 6 A	S203P-C6	2CDS283001R0064	ABB
-F1;-F2	2	Miniature Circuit Breaker - S202- 2P - C - 6 A	S202-C6	2CDS252001R0064	ABB
-Fan	1	PT PANEL FAN WITH FILTER 160X160	PTF	PTF1500	Plastim
-Fan	1	PT FILTER FOR FAN 160X160	PTI	PTI1500	Plastim
-H1;-H3	2	Monolithic pilot light Ø 22 - Green - integral LED - 230V		HLD1122C41N3	himel
-H2;-H4	2	Monolithic pilot light Ø 22 - Red - integral LED - 230V		HLD1122C41N4	himel
-M2	1	Metal Enclosure 700H x 600W x300D IP65 RAL7035	ER	ER706030D	
PLC	1	Logo PLC 8 inputs / 4outputs with display 24V AC/DC	6ED1052-1HB08-0BA0	6ED1052-1HB08-0BA0	SIE
-PSU	1	Power supply unit 230V AC/24Vdc 2.5A		HDR-60-24	meanwell
-Q0	1	OT40F3 switch-disconnector	OT40F3	1SCA104902R1001	ABB
-Q0	1	OHBS2AJ1 SELECTOR HANDLE	OHBS2AJ1	1SCA105215R1001	ABB
-Q0	1	OXS6X180 SHAFT for selector handle	OXS6X180	1SCA101659R1001	ABB
-1R1;-1RV1;-1RV2;-2R1;-2RV1;-2RV2	6	CR-M230AC4 Pluggable interface relay 4c/o, A1-A2=230VAC, 250V/6A	CR-M230AC4	1SVR405613R3000	ABB
-1R1;-1RV1;-1RV2;-2R1;-2RV1;-2RV2	6	CR-M4SS Standard socket for 2c/o or 4c/o CR-M relay	CR-M4SS	1SVR405651R3000	ABB
-S1;-S2	2	SELECTOR SWITCH 230VAC	HLAY5ED33	HLAY5ED33	Himel
-S1;-S2	2	CONTACT BLOCK BE101 NO contact	HLAY5BE101	HLAY5BE101	Himel
-TH1	1	Thermostat for fan 1NO	PTVT	PTVT	Plastim
U1;U2	2	Variable frequency drive 3.0kW IP20 Bultin RFI, Bultin DC Choke,W/out Keypad, Modbus, BACnet	FC-101P3K0	131L9865	Danfoss
-X11;-X12	22	Feed-through terminal block	TB 2,5 EI	3246010	PXC

COR 2 HelixV1006 Logo-M -AE		A.N	 Wilo Middle East FZE Jebel Ali Free Zone–South PO Box 262720 Dubai UAE Tel: (+971 4) 880 91 77 Fax: (+971 4) 880 91 88. Ext. 122			
		CHECKED BY				
		S.S				
		TITLE	PROJECT	DRAWN		
		6/15/2022			000	9 /12
CONSULTANT	CLIENT	DATE	SCALE	DRAWING NO	REV	PAGE

Mechanical Assembly

Pump Type : Helix V 1006-2/25/V/KS/400-50

Pump Article number : 4150577

Number of Pumps : 2

Rated power : 2.2kW

System Voltage : 3 x 400V AC 50Hz



System Max. pressure : 25 bar

Range : Standard

Speed : Variable speed

Adder:
SS316 manifold

COR 2 HelixV1006 Logo-M -AE		A.N	 Wilo Middle East FZE Jebel Ali Free Zone–South PO Box 262720 Dubai UAE Tel: (+971 4) 880 91 77 Fax: (+971 4) 880 91 88. Ext. 122			
		CHECKED BY				
		S.S				
TITLE	PROJECT					
		DRAWN			000	10 /12
		6/15/2022				
CONSULTANT	CLIENT	DATE	SCALE	DRAWING NO	REV	PAGE

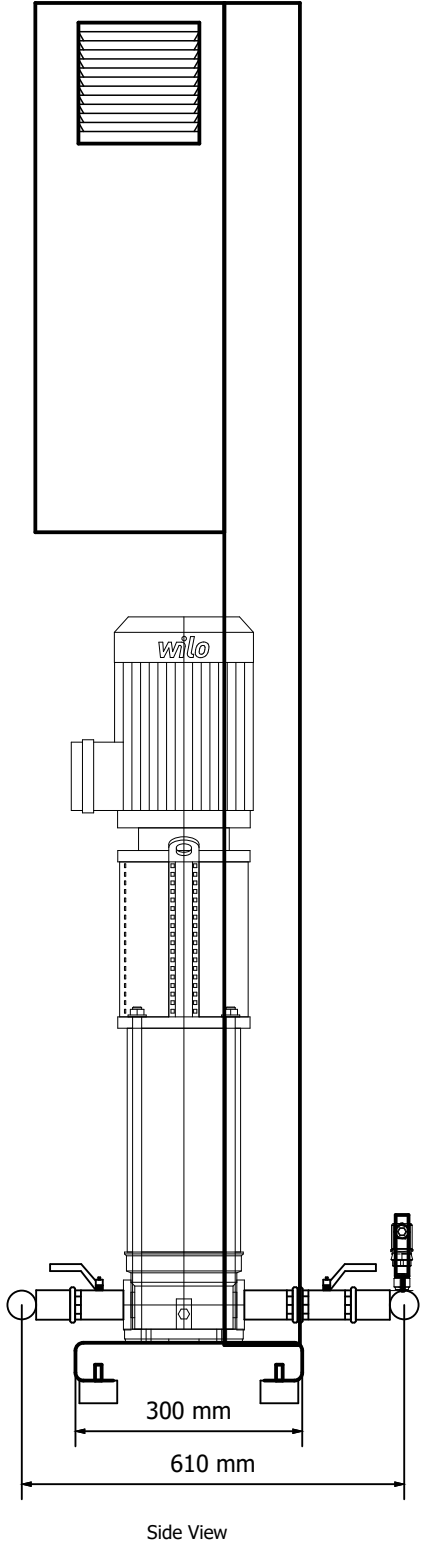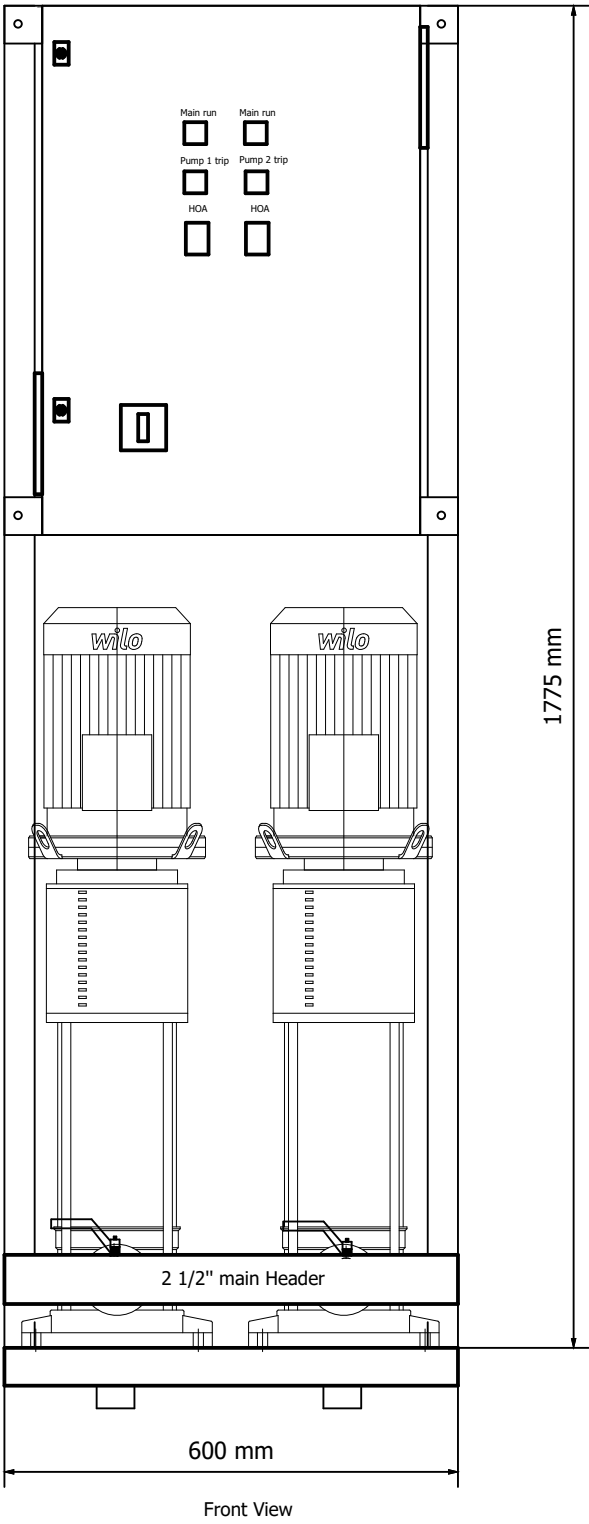

COR 2 HelixV1006 Logo-M -AE		A.N	wilo Wilo Middle East FZE Jebel Ali Free Zone-South PO Box 262720 Dubai UAE Tel: (+971 4) 880 91 77 Fax: (+971 4) 880 91 88. Ext. 122			
		CHECKED BY				
TITLE	PROJECT	S.S				
		DRAWN				
		6/15/2022			000	11 /12
CONSULTANT	CLIENT	DATE	SCALE	DRAWING NO	REV	PAGE

Mechanical Assembly

Description	Type number	Qty	Supplier
Suction header SS316 2 1/2" 2 x 1 1/2" threaded PN16 300mm	A250/150	1	Wilo
Delivery header SS316 2 1/2" 2 x 1 1/2" threaded PN16 300mm	M250/150	1	Wilo
Check Valve 1 1/2" Brass	-	2	Enolgas
MF Ball Valve 1 1/2"	-	4	Enolgas
Pressure Gauge 0 -10Bar		1	-
PRESS.SENSOR 1/4"0-16BAR 4-20MA M12 T528	2541620	1	Wilo
HEXAGON CAP 2"		2	-
BASE-FRAME-EB-2*2/4/8/16H-2*2/4V-E300	4066173	1	Wilo
VIBRATION DAMPER 50x30mm,M10x28 Form D	502555494	4	Wilo
BRACKET-EB-2&3 V-CV-H=1775	4066185	2	Wilo
PLASTIC PLUG 80X40 PE GPN R8040	2500189	2	Wilo

COR 2 HelixV1006 Logo-M -AE		A.N	wilo Wilo Middle East FZE Jebel Ali Free Zone-South PO Box 262720 Dubai UAE Tel: (+971 4) 880 91 77 Fax: (+971 4) 880 91 88. Ext. 122			
		CHECKED BY				
TITLE	PROJECT	S.S			000	12 /12
		DRAWN				
		6/15/2022				
CONSULTANT	CLIENT	DATE	SCALE	DRAWING NO	REV	PAGE