



COR 2Helix V604/Logo-M-AE

Number of Pumps	:	2
Rated Power	:	0.75kW
Rated Current	:	1.7A
Supply rating	:	3 x400V 50Hz
Duty/Assist/Standby	:	1D+1S
Starting Method	:	Multi VFD
IP rating	:	IP54
Ambient Temp.	:	50 deg C
Article Number	:	XXXXXX
Project Name	:	SAKHIR PROJECT
Application	:	Booster set


Additional Specification:

COR 2 HelixV604 Logo-M -AE		A.N	wilo Wilo Middle East FZE Jebel Ali Free Zone–South PO Box 262720 Dubai UAE Tel: (+971 4) 880 91 77 Fax: (+971 4) 880 91 88. Ext. 122			
		CHECKED BY				
		S.S				
TITLE	PROJECT					
		DRAWN			000	1 /12
		6/15/2022				
CONSULTANT	CLIENT	DATE	SCALE	DRAWING NO	REV	PAGE


TECHNICAL DATA SHEET

ENCLOSURE SCHNEIDER ALFANAR LOCAL GRP MATERIAL SHEET STEEL STAINLESS STEEL ALUMINUM GRP PRESENTATION FIXED FRONT FUNCTIONAL DOOR PLAIN DOOR TRANSPARENT DOOR OTHER TYPE OF CONSTRUCTION FORM - 1 FORM - 3 FORM - 4 DIMENSION (in mm) HEIGHT : 700 WIDTH : 600 DEPTH : 300 COLOUR RAL 7032 RAL 7035 MOUNTING WALL FLOOR PEDESTAL INSTALLATION INDOOR APPLICATION OUTDOOR APPLICATION			NEUTRAL/EARTH SYSTEM: DIRECT TO EARTH (TT) SEPARATE (TN-S) EARTHED (TN-C) ISOLATED (IT) BUS BARS HARD DRAWN HIGH CONDUCTIVITY COPPER ELECTROLYTICALLY TINNED BUSBARS SUITABLY SIZED MAIN(VER.) Size(XXXX) MAIN(HOR.) Size(XXXX) NEUTRAL Size(XXXX) EARTH Size(XXXX) BRANCH Size(XXXX) INSULATION VOLTAGE UPTO 600V CONNECTIONS TERMINATION DIRECT TO DEVICE THRU TERMINAL BLOCKS ACCESS FRONT REAR LEFT SIDE/ RIGHT SIDE CABLE ENTRY TOP BOTTOM SHROUDING ALL LIVE PARTS WIRING CONTROL 1.0 Sqmm C.T WIRES 2.5Sqmm			AUXILIARY SUPPLY VOLTAGE 240V AC 220V AC 110V AC 24V AC 24V DC ORIGIN EXTERNAL INTERNAL AUXILIARY TRANSFORMER AUXILIARY DC SOURCE CIRCUIT MARKING WIRING > Power Cable : Phase : Upto - 16sqmm - Red, yellow, Blue Above 16sqmm - black cable with color code sleeve Neutral : Black Earth : Yellow + Green Control Cable : 230V AC : Red+Black 110V AC : Orange 24VAC : Grey 12V/24V DC : Blue(+), White(-) Volt Free contact : Brown LABELS FACIA LEGEND PLATES OF 1.5mm PRINTED PVC WITH WHITE LETTERS ON BLACK BACKGROUND ALL LABELS WITH CHAMFERED EDGES DANGER LABELS WITH WHITE LETTERS ON RED BACKGROUND			Standard Specification: Door interlock Isolator Motor overload protection Base load pump VFD control Pump run hour Equalizer Trip changeover standby changeover Dry run interlock System enable/disable Low/high pressure cutoff Door components: Run, Trip indication lamp HOA switch per pump BMS: VFC contact: Run, Trip, Auto per pump TYPE OF DRAWING ISSUED FOR APPROVAL ISSUED FOR PRODUCTION AS BUILT DRAWING ALL DIMENSIONS ARE IN mm		
--	--	--	---	--	--	--	--	--	---	--	--


COR 2 HelixV604 Logo-M -AE		A.N		 Wilo Middle East FZE Jebel Ali Free Zone–South PO Box 262720 Dubai UAE Tel: (+971 4) 880 91 77 Fax: (+971 4) 880 91 88. Ext. 122			
		CHECKED BY					
		S.S					
TITLE	PROJECT	DRAWN				000	2 /12
		6/15/2022					
CONSULTANT	CLIENT	DATE	SCALE	DRAWING NO		REV	PAGE

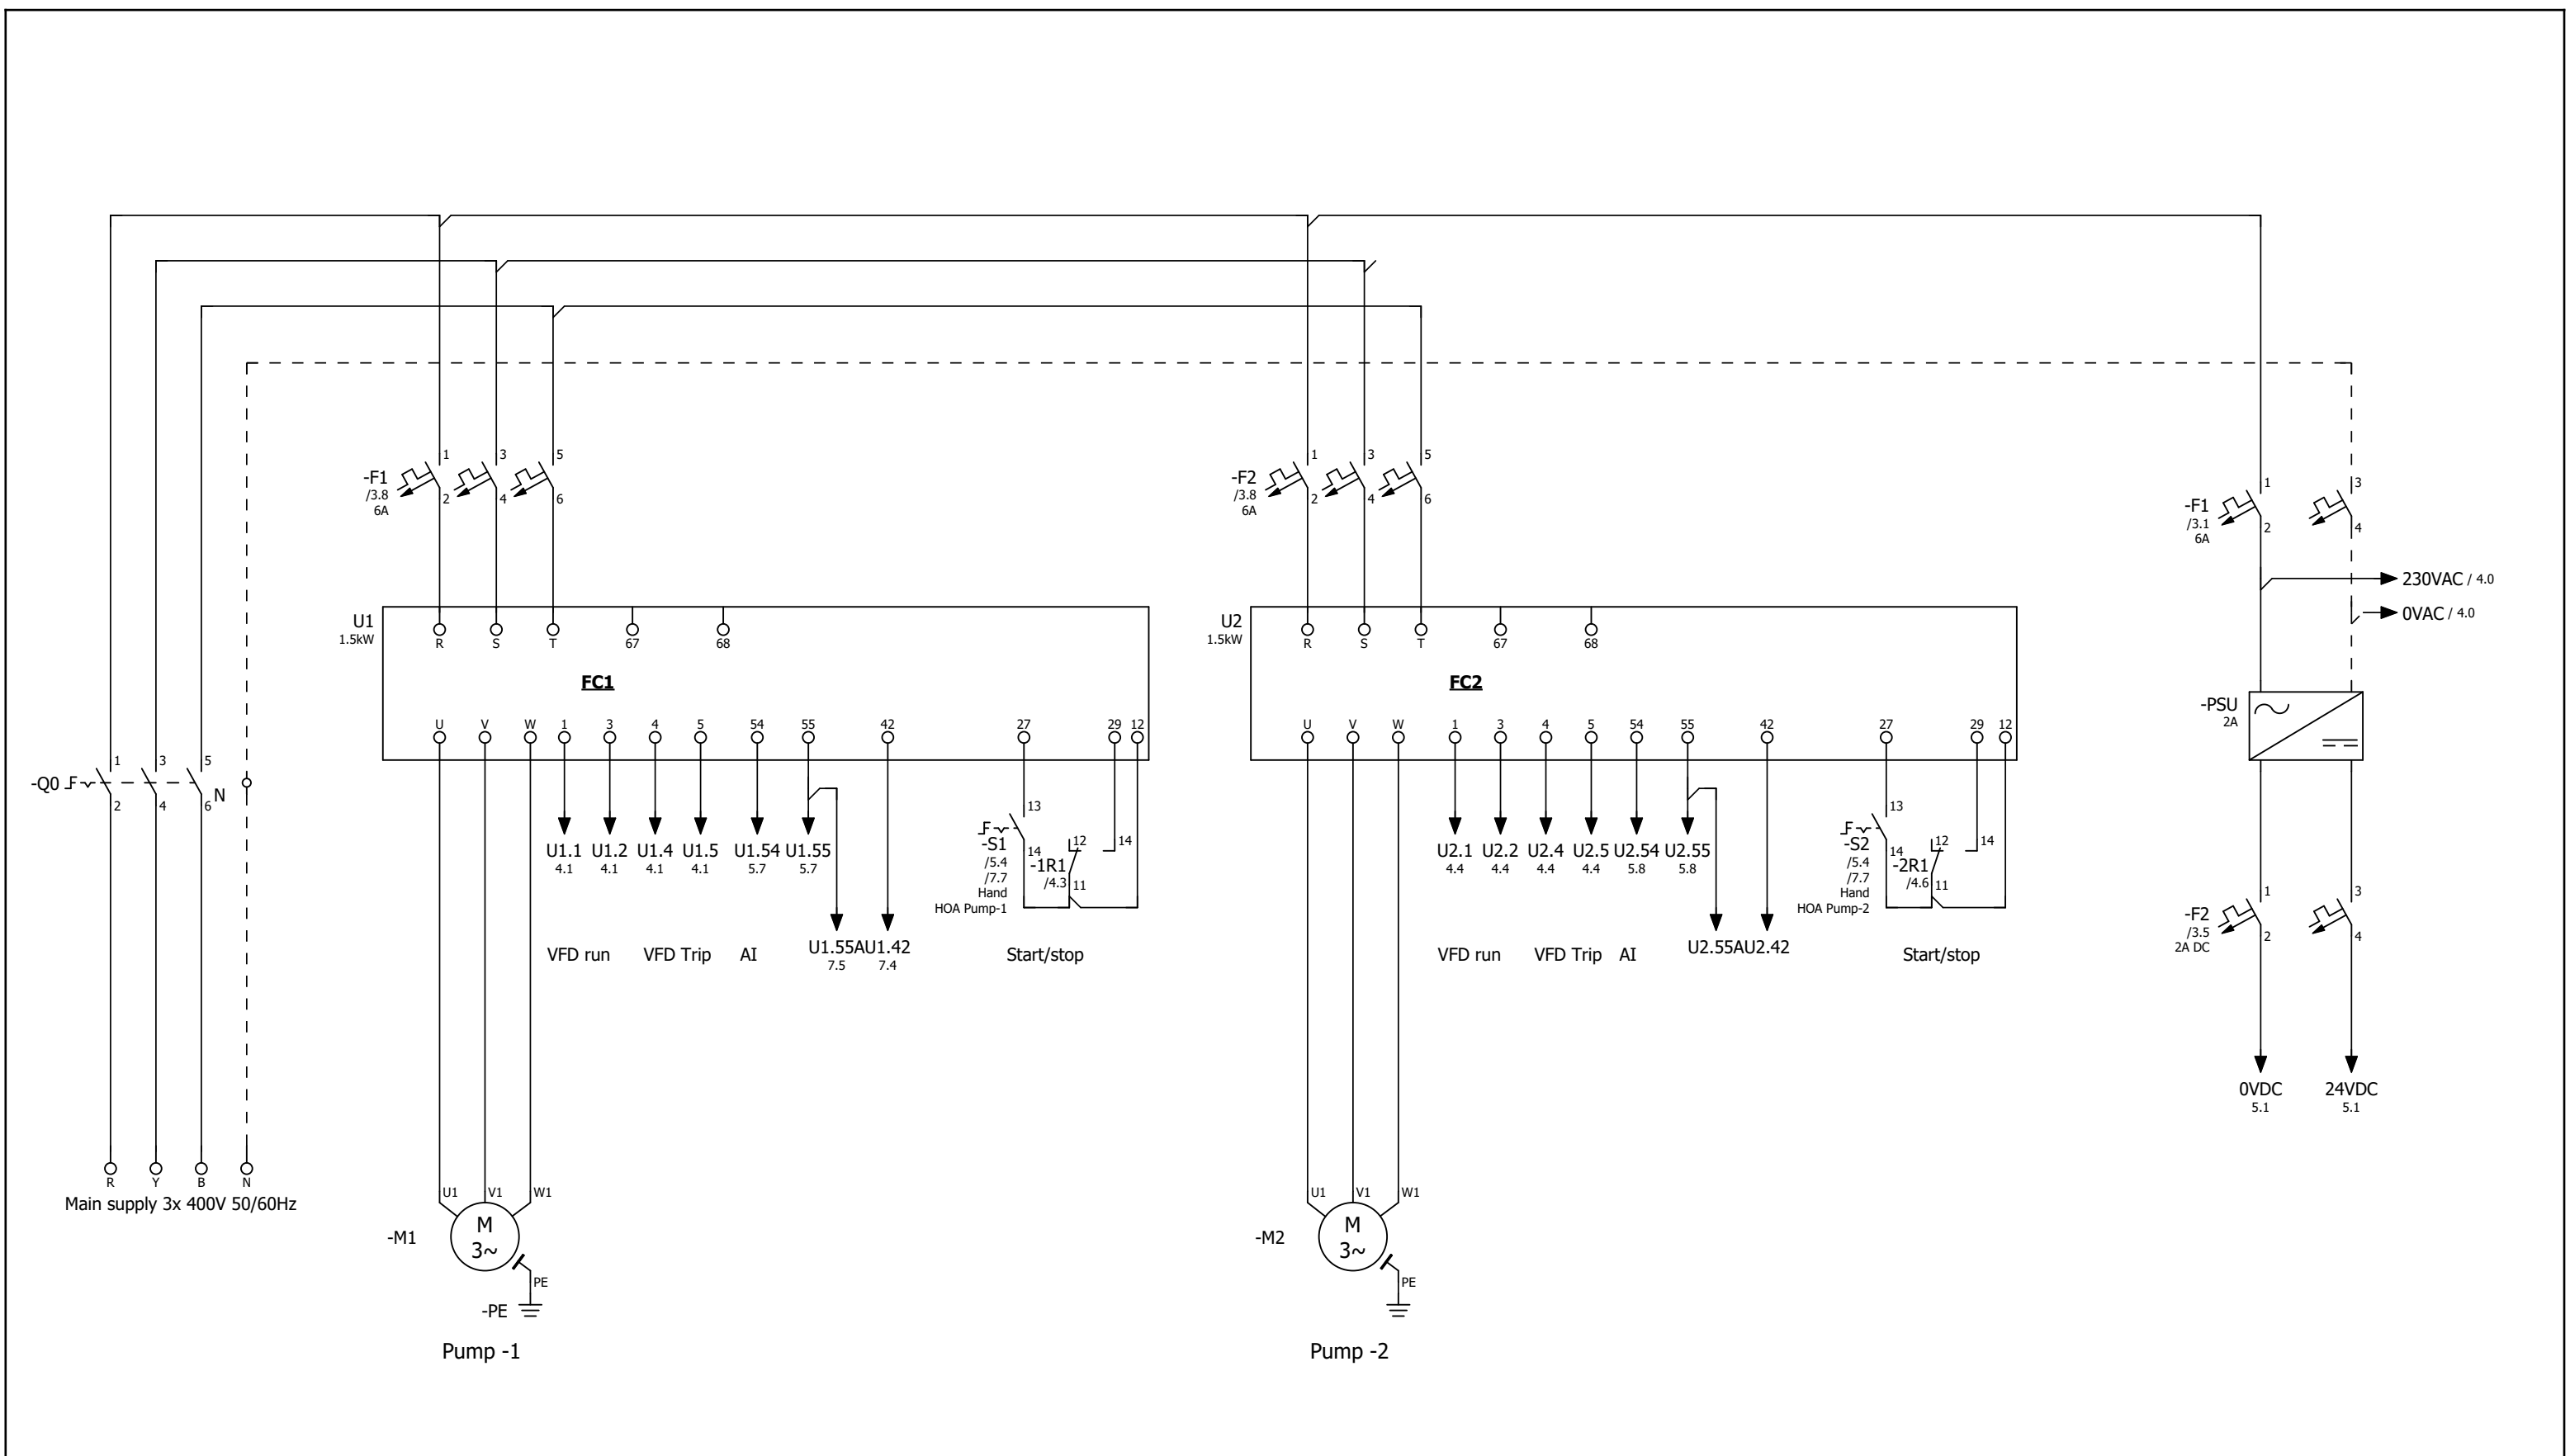

COR 2 HelixV604 Logo-M -AE		A.N	wilo Wilo Middle East FZE Jebel Ali Free Zone-South PO Box 262720 Dubai UAE Tel: (+971 4) 880 91 77 Fax: (+971 4) 880 91 88. Ext. 122				
TITLE	PROJECT	S.S	DRAWN	6/15/2022			
CONSULTANT	CLIENT	DATE	SCALE	DRAWING NO	REV	000	3 /12

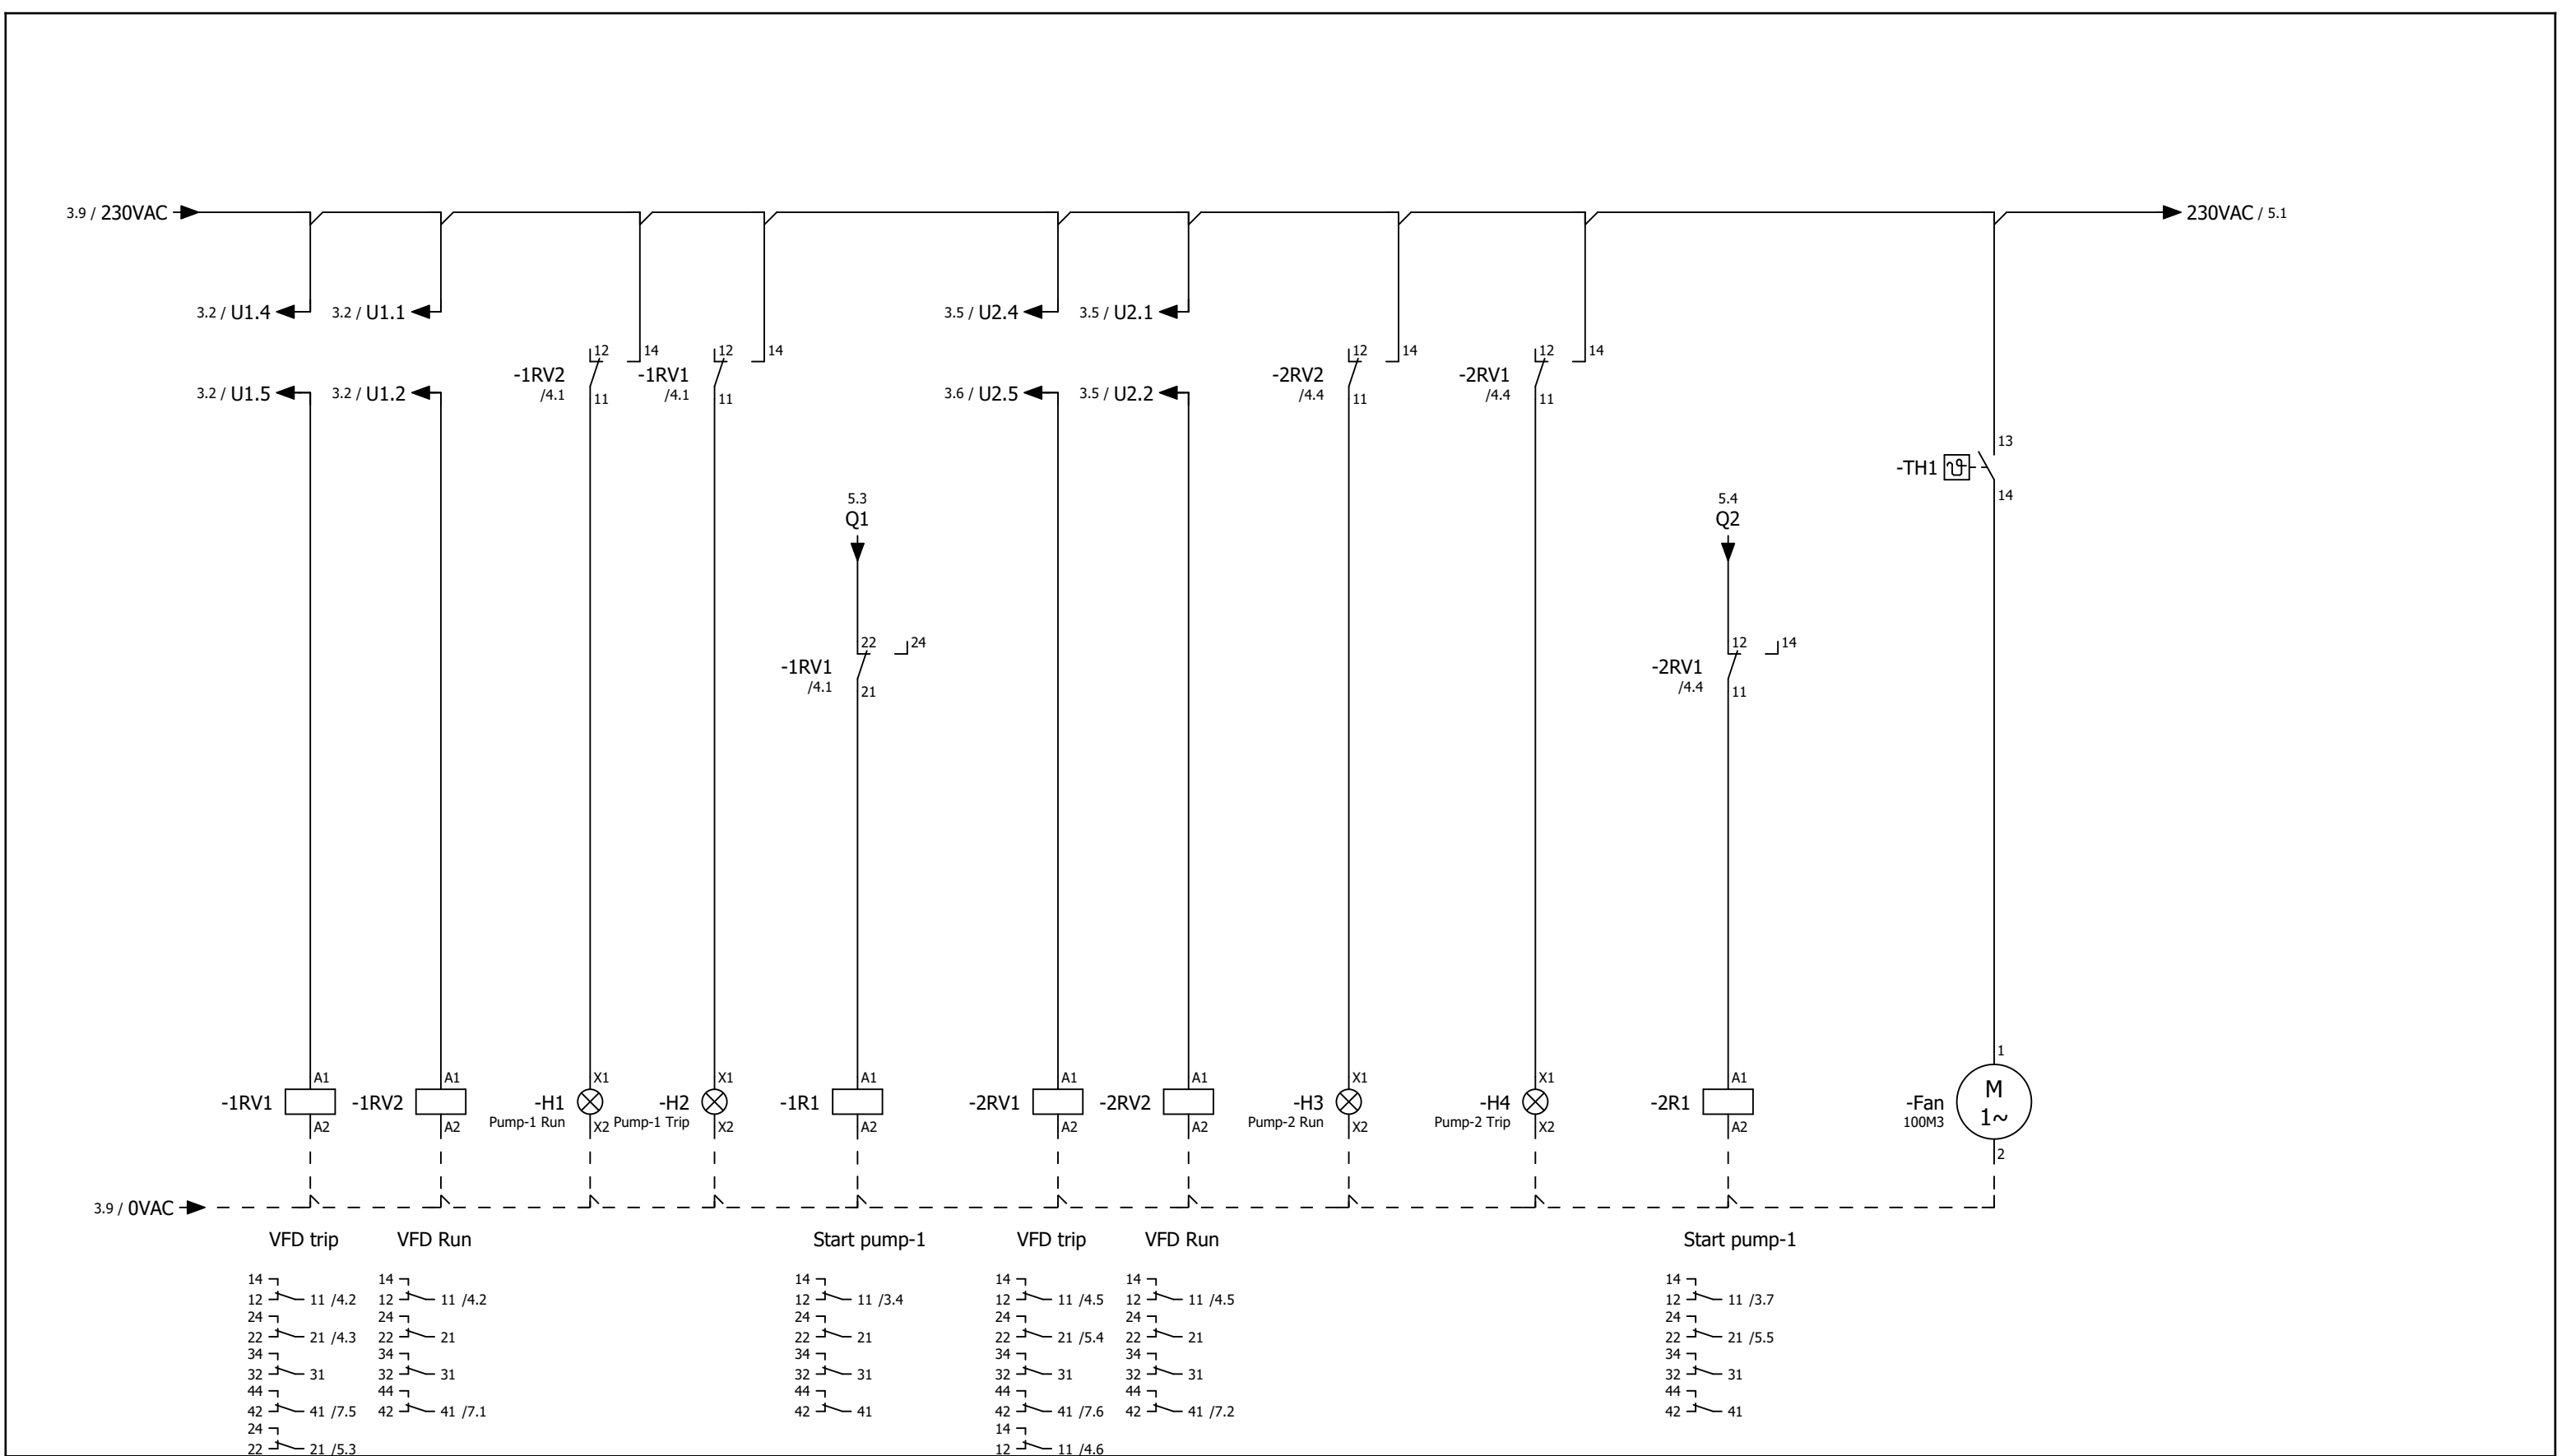


COR 2 HelixV604 Logo-M -AE		A.N	wilo Wilo Middle East FZE Jebel Ali Free Zone-South PO Box 262720 Dubai UAE Tel: (+971 4) 880 91 77 Fax: (+971 4) 880 91 88. Ext. 122				
		CHECKED BY					
		S.S					
TITLE	PROJECT		DRAWN			000	4 /12
		6/15/2022					
CONSULTANT	CLIENT	DATE	SCALE	DRAWING NO	REV	PAGE	

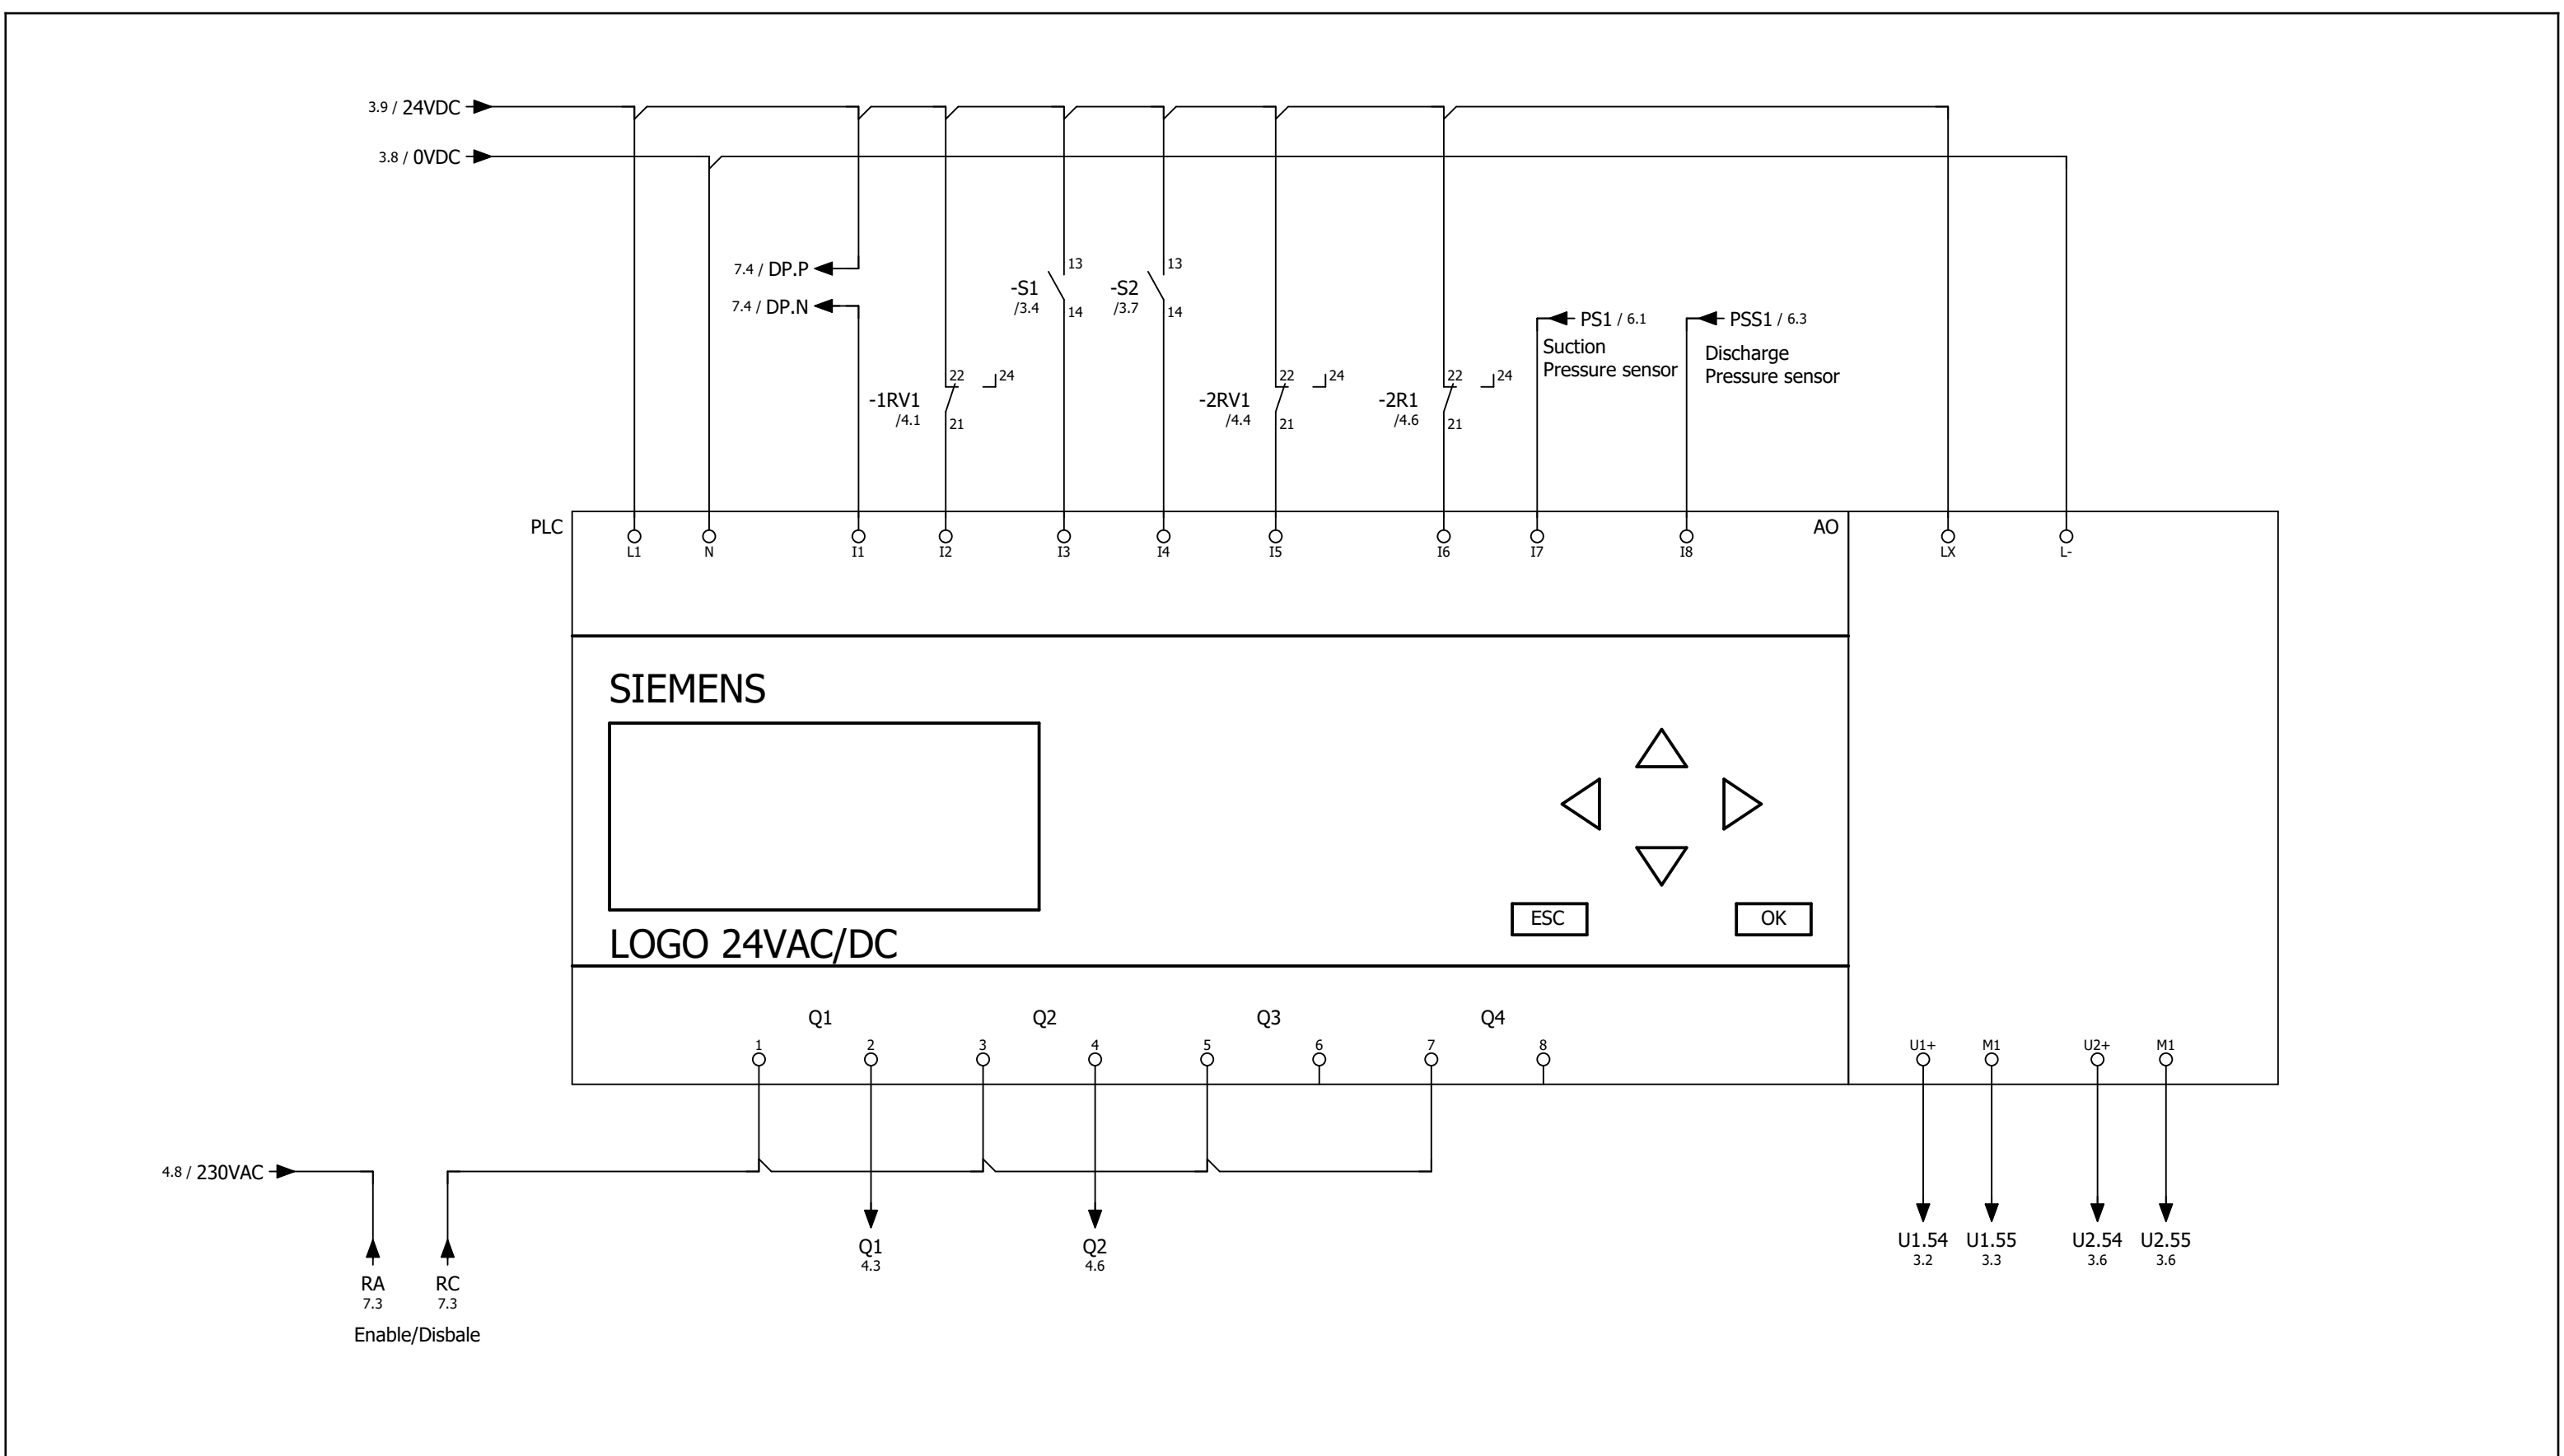


COR 2 HelixV604 Logo-M -AE		A.N	 Wilo Middle East FZE Jebel Ali Free Zone-South PO Box 262720 Dubai UAE Tel: (+971 4) 880 91 77 Fax: (+971 4) 880 91 88. Ext. 122			
		CHECKED BY				
		S.S				
TITLE	PROJECT	DRAWN			000	5 /12
	6/15/2022					
CONSULTANT	CLIENT	DATE	SCALE	DRAWING NO	REV	PAGE


Pressure Transmitter Signal:

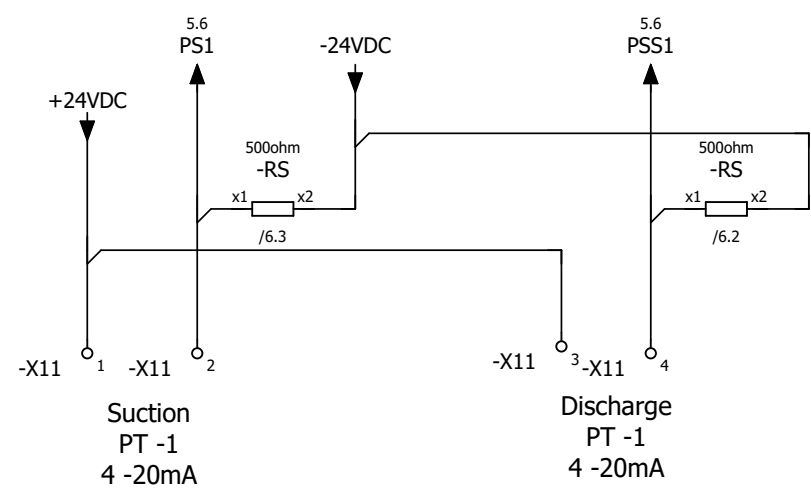


COR 2 HelixV604 Logo-M -AE		A.N	wilo Wilo Middle East FZE Jebel Ali Free Zone-South PO Box 262720 Dubai UAE Tel: (+971 4) 880 91 77 Fax: (+971 4) 880 91 88. Ext. 122			
		CHECKED BY				
		S.S				
TITLE	PROJECT	DRAWN			000	6 /12
		6/15/2022				
CONSULTANT	CLIENT	DATE	SCALE	DRAWING NO	REV	PAGE

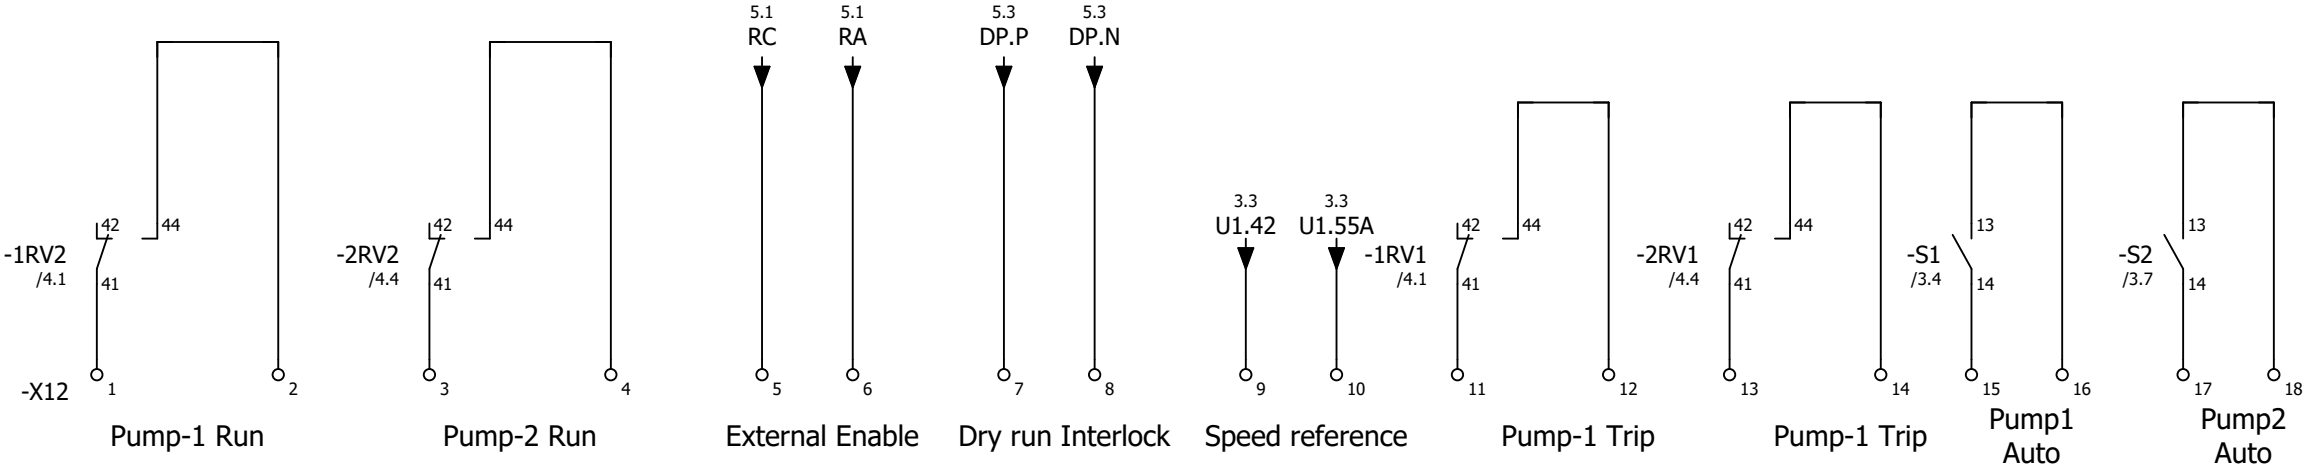


COR 2 HelixV604 Logo-M -AE		A.N	 Wilo Middle East FZE Jebel Ali Free Zone–South PO Box 262720 Dubai UAE Tel: (+971 4) 880 91 77 Fax: (+971 4) 880 91 88. Ext. 122			
		CHECKED BY				
		S.S				
TITLE	PROJECT					
		DRAWN				
		6/15/2022			000	7 /12
CONSULTANT	CLIENT	DATE	SCALE	DRAWING NO	REV	PAGE

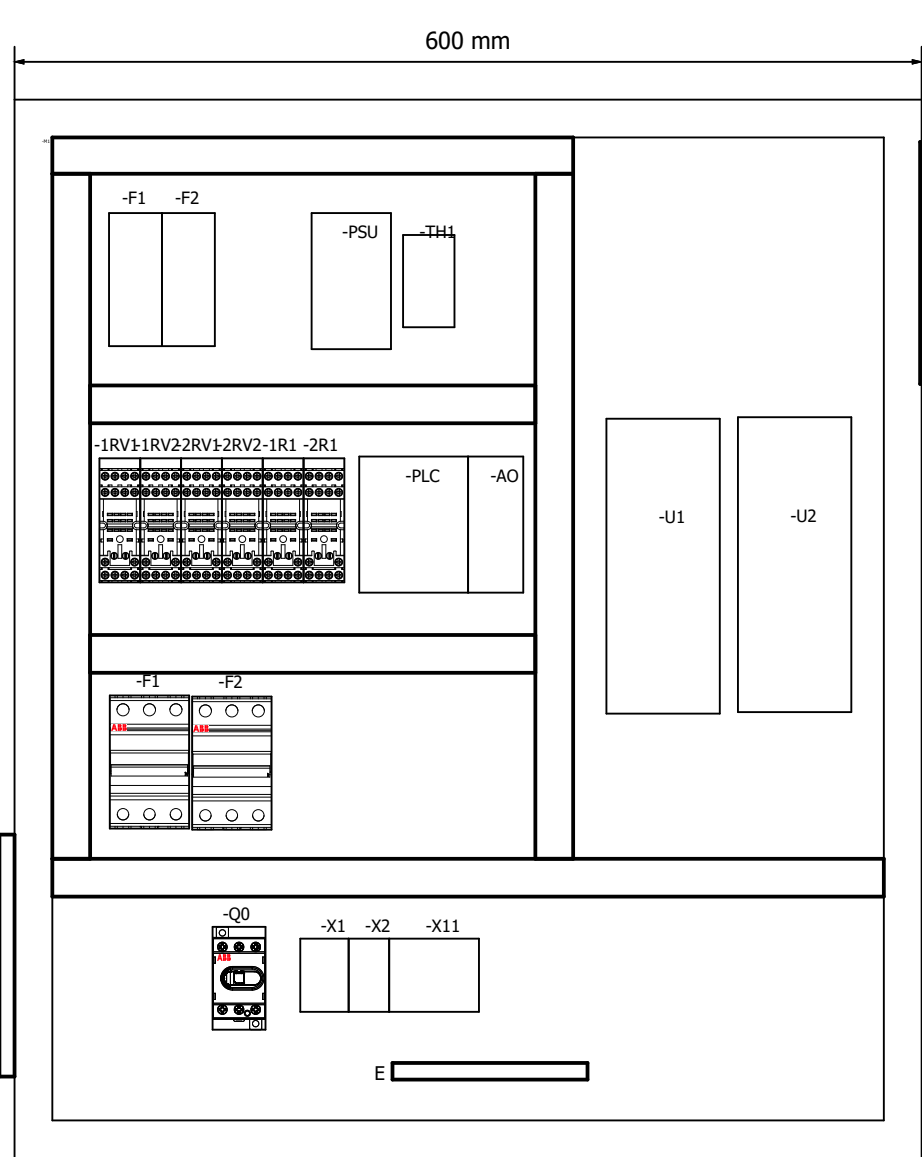

Internal View

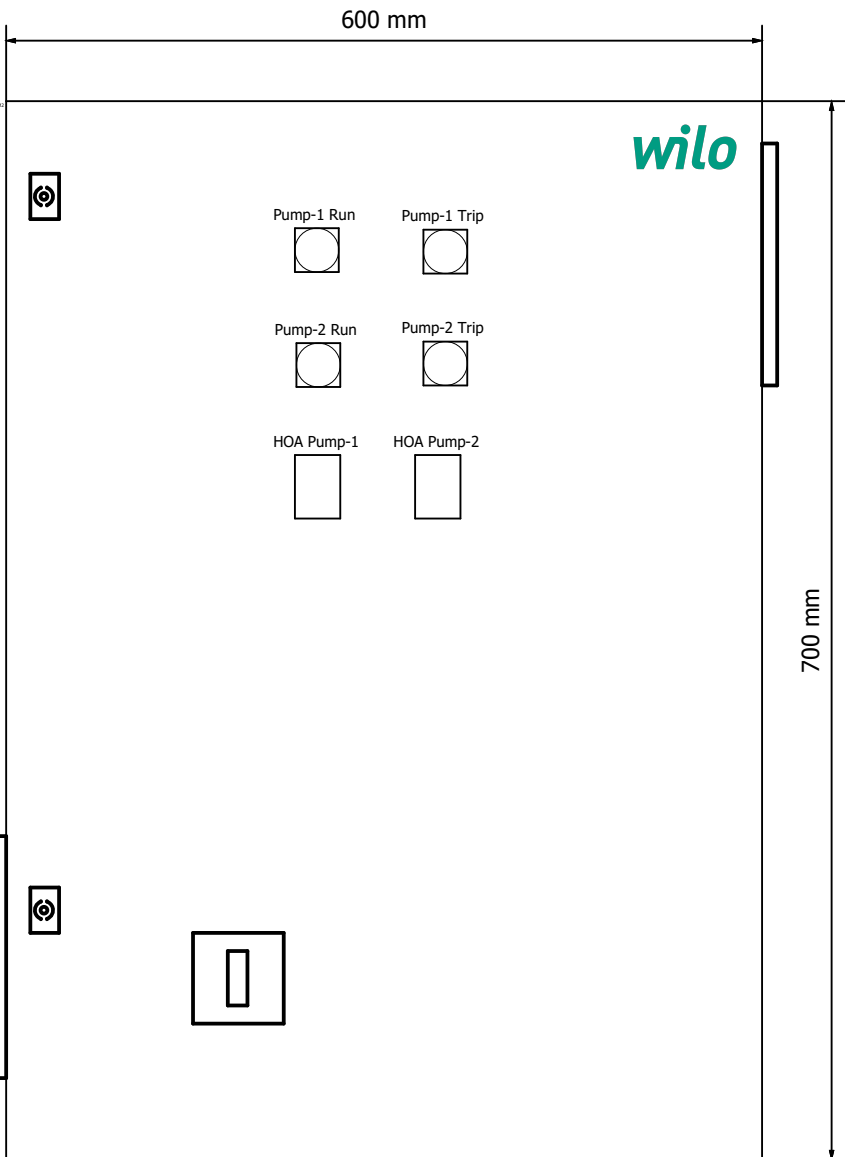

Front Fascia

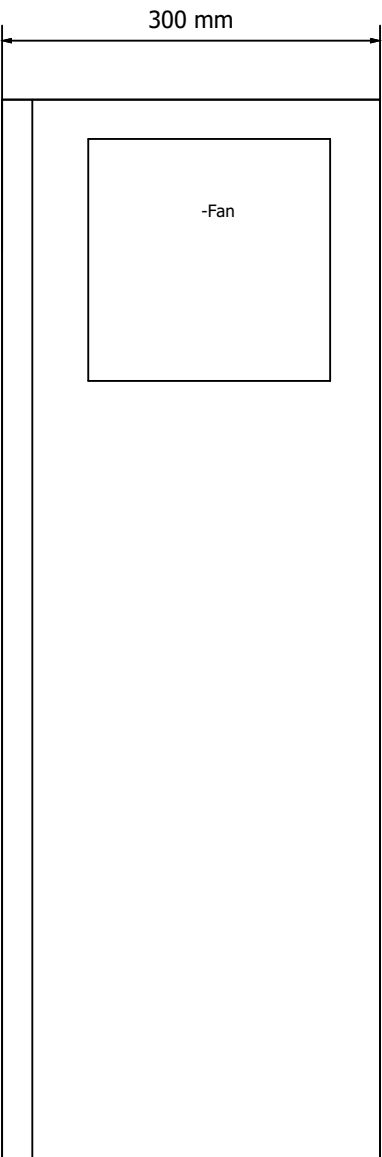

Side view

COR 2 HelixV604 Logo-M -AE		A.N	wilo Wilo Middle East FZE Jebel Ali Free Zone–South PO Box 262720 Dubai UAE Tel: (+971 4) 880 91 77 Fax: (+971 4) 880 91 88. Ext. 122			
		CHECKED BY				
		S.S				
TITLE	PROJECT					
		DRAWN			000	
		6/15/2022				
CONSULTANT	CLIENT	DATE	SCALE	DRAWING NO	REV	PAGE
						8 /12

Summarized parts list

Device Tag	Quantity	Designation	Type number	Order number	Supplier
AO	1	LOGO! AM2 AQ expansion module, PS: 24 V DC, 2 AO, 0-10 V, 0/4-20 mA for LOGO! 8	6ED1055-1MM00-0BA2	6ED1055-1MM00-0BA2	SIE
-F1;-F2	2	Miniature Circuit Breaker - S200P - 3P - C - 6 A	S203P-C6	2CDS283001R0064	ABB
-F1;-F2	2	Miniature Circuit Breaker - S202- 2P - C - 6 A	S202-C6	2CDS252001R0064	ABB
-Fan	1	PT PANEL FAN WITH FILTER 160X160	PTF	PTF1500	Plastim
-Fan	1	PT FILTER FOR FAN 160X160	PTI	PTI1500	Plastim
-H1;-H3	2	Monolithic pilot light Ø 22 - Green - integral LED - 230V		HLD1122C41N3	himel
-H2;-H4	2	Monolithic pilot light Ø 22 - Red - integral LED - 230V		HLD1122C41N4	himel
-M2	1	Metal Enclosure 700H x 600W x300D IP65 RAL7035	ER	ER706030D	
PLC	1	Logo PLC 8 inputs / 4outputs with display 24V AC/DC	6ED1052-1HB08-0BA0	6ED1052-1HB08-0BA0	SIE
-PSU	1	Power supply unit 230V AC/24Vdc 2.5A		HDR-60-24	meanwell
-Q0	1	OT40F3 switch-disconnector	OT40F3	1SCA104902R1001	ABB
-Q0	1	OHBS2AJ1 SELECTOR HANDLE	OHBS2AJ1	1SCA105215R1001	ABB
-Q0	1	OXS6X180 SHAFT for selector handle	OXS6X180	1SCA101659R1001	ABB
-1R1;-1RV1;-1RV2;-2R1;-2RV1;-2RV2	6	CR-M230AC4 Pluggable interface relay 4c/o, A1-A2=230VAC, 250V/6A	CR-M230AC4	1SVR405613R3000	ABB
-1R1;-1RV1;-1RV2;-2R1;-2RV1;-2RV2	6	CR-M4SS Standard socket for 2c/o or 4c/o CR-M relay	CR-M4SS	1SVR405651R3000	ABB
-S1;-S2	2	SELECTOR SWITCH 230VAC	HLAY5ED33	HLAY5ED33	Himel
-S1;-S2	2	CONTACT BLOCK BE101 NO contact	HLAY5BE101	HLAY5BE101	Himel
-TH1	1	Thermostat for fan 1NO	PTVT	PTVT	Plastim
U1;U2	2	Variable frequency drive 1.5kW IP20 Bultin RFI, Bultin DC Choke,W/out Keypad, Modbus, BACnet	FC-101P1K5	131L9863	Danfoss
-X11;-X12	22	Feed-through terminal block	TB 2,5 EI	3246010	PXC

COR 2 HelixV604 Logo-M -AE		A.N	wilo Wilo Middle East FZE Jebel Ali Free Zone–South PO Box 262720 Dubai UAE Tel: (+971 4) 880 91 77 Fax: (+971 4) 880 91 88. Ext. 122			
		CHECKED BY				
		S.S				
TITLE	PROJECT					
		DRAWN				
		6/15/2022			000	9 /12
CONSULTANT	CLIENT	DATE	SCALE	DRAWING NO	REV	PAGE

Mechanical Assembly

Pump Type : HELIX V604/25/V/KS/400-50

Pump Article number : 4160552

Number of Pumps : 2

Rated power : 0.75kW

System Voltage : 3 x 400V AC 50Hz



System Max. pressure : 25 bar

Range : Standard

Speed : Variable speed

Adder:
SS316 manifold

COR 2 HelixV604 Logo-M -AE		A.N	wilo Wilo Middle East FZE Jebel Ali Free Zone–South PO Box 262720 Dubai UAE Tel: (+971 4) 880 91 77 Fax: (+971 4) 880 91 88. Ext. 122			
		CHECKED BY				
		S.S				
TITLE	PROJECT					
		DRAWN			000	10 /12
		6/15/2022				
CONSULTANT	CLIENT	DATE	SCALE	DRAWING NO	REV	PAGE

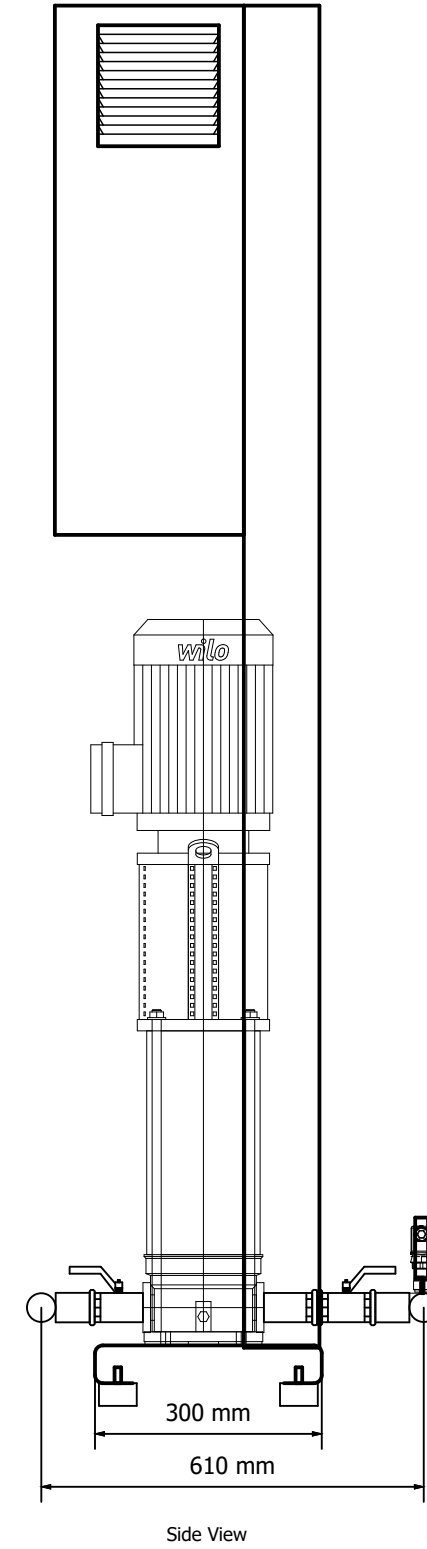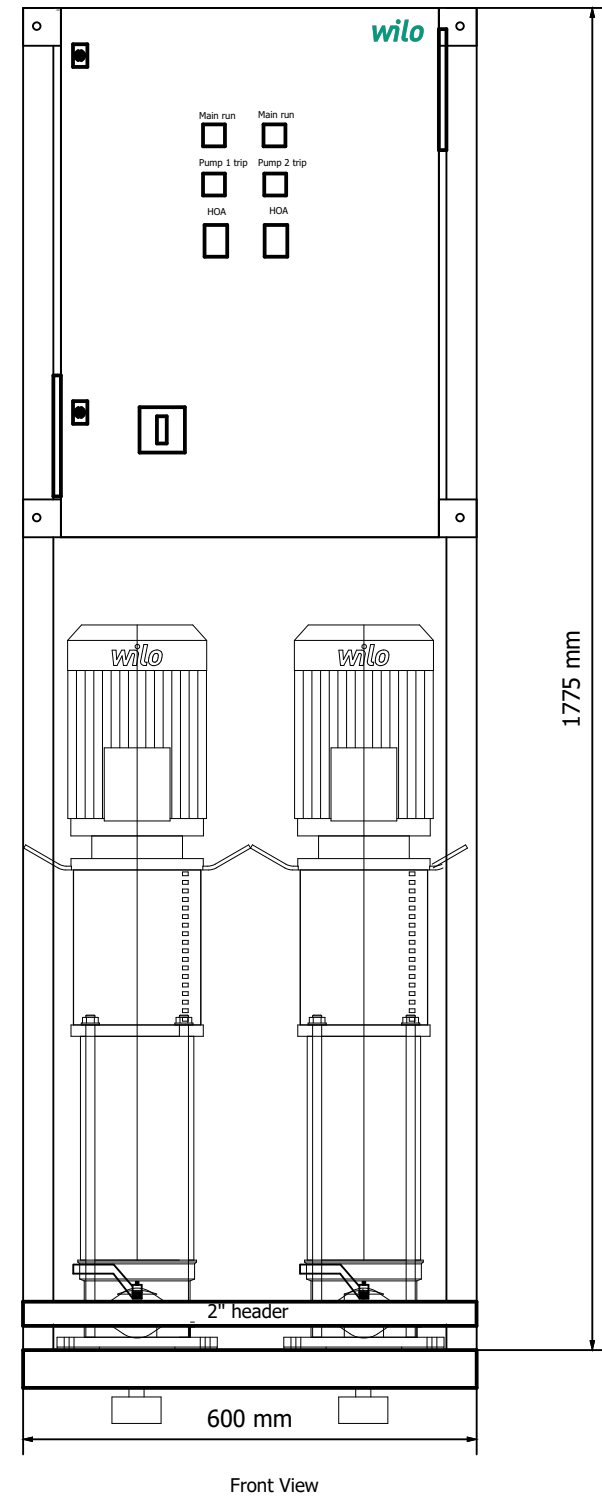

COR 2 HelixV604 Logo-M -AE		A.N	wilo Wilo Middle East FZE Jebel Ali Free Zone-South PO Box 262720 Dubai UAE Tel: (+971 4) 880 91 77 Fax: (+971 4) 880 91 88. Ext. 122				
		CHECKED BY					
		S.S					
TITLE	PROJECT	DRAWN				000	11 /12
	6/15/2022						
CONSULTANT	CLIENT	DATE	SCALE	DRAWING NO	REV	PAGE	

Mechanical Assembly

Description	Type number	Qty	Supplier
Suction header SS316 2" 2 x 1 1/4" threaded PN16 300mm	A200/125	1	Wilo
Delivery header SS316 2" 2 x 1 1/4" threaded PN16 300mm	M200/125	1	Wilo
Check Valve 1 1/4" Brass	-	2	Enolgas
MF Ball Valve 1 1/4"	-	4	Enolgas
Pressure Gauge 0 -10Bar		1	-
PRESS.SENSOR 1/4"0-16BAR 4-20MA M12 T528	2541620	1	Wilo
HEXAGON CAP 2"		2	-
BASE-FRAME-EB-2*2/4/8/16H-2*2/4V-E300	4066173	1	Wilo
VIBRATION DAMPER 50x30mm,M10x28 Form D	502555494	4	Wilo
BRACKET-EB-2&3 V-CV-H=1775	4066185	2	Wilo
PLASTIC PLUG 80X40 PE GPN R8040	2500189	2	Wilo

COR 2 HelixV604 Logo-M -AE		A.N	 Wilo Middle East FZE Jebel Ali Free Zone-South PO Box 262720 Dubai UAE Tel: (+971 4) 880 91 77 Fax: (+971 4) 880 91 88. Ext. 122			
		CHECKED BY				
TITLE	PROJECT	S.S			000	12 /12
		DRAWN				
		6/15/2022				
CONSULTANT	CLIENT	DATE	SCALE	DRAWING NO	REV	PAGE